

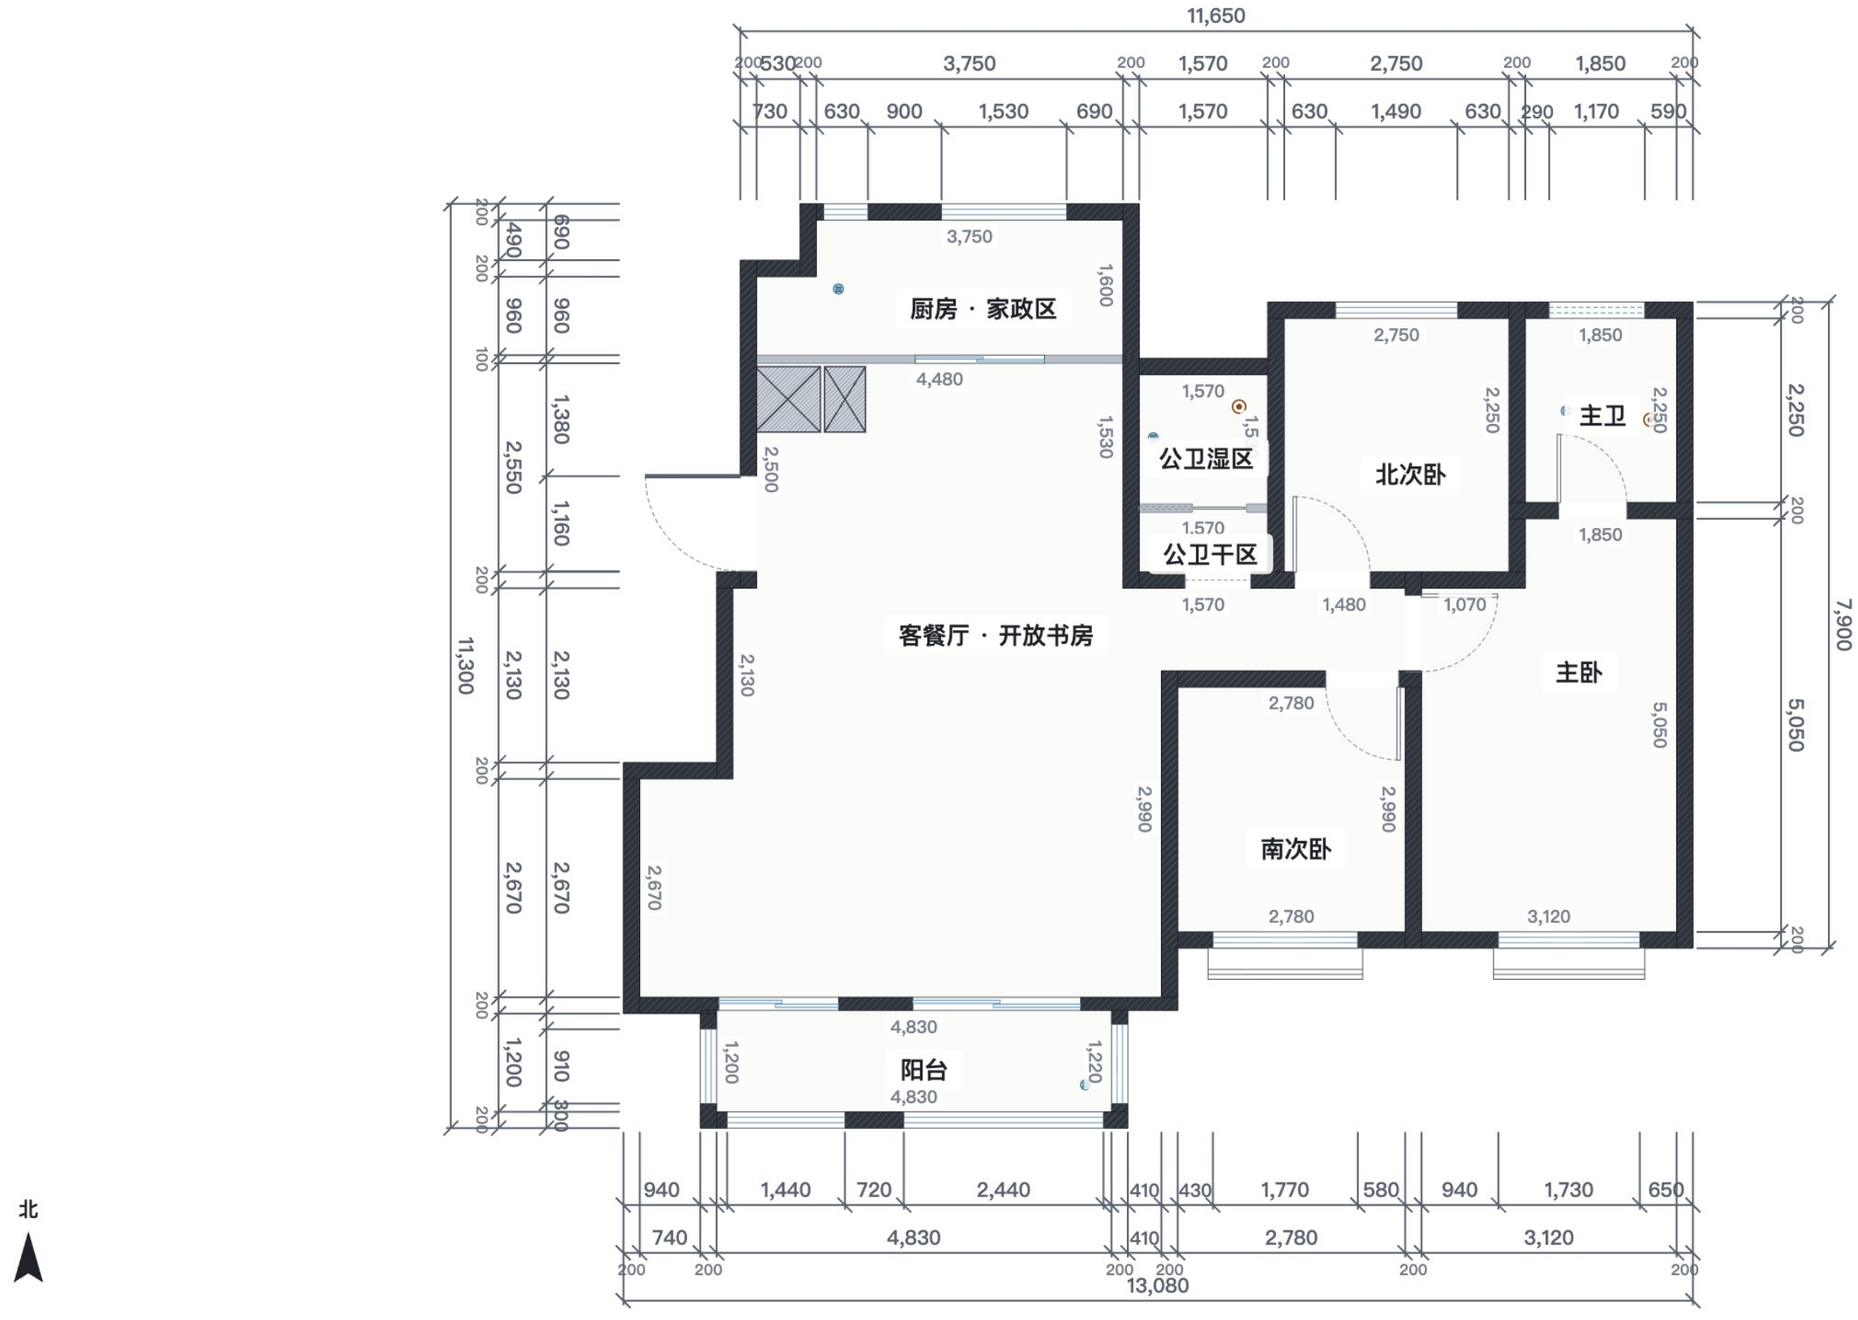


项目名称 D户型128㎡ · 四室两厅两卫	比例 1:75	单位 mm
图名 原始结构图	日期 2026/11/10	图号 01 / 32

原有承重墙　原有隔墙　新砌墙　拆除墙　新砌 0.00 m · 拆除 0.00 m（墙中线长度）

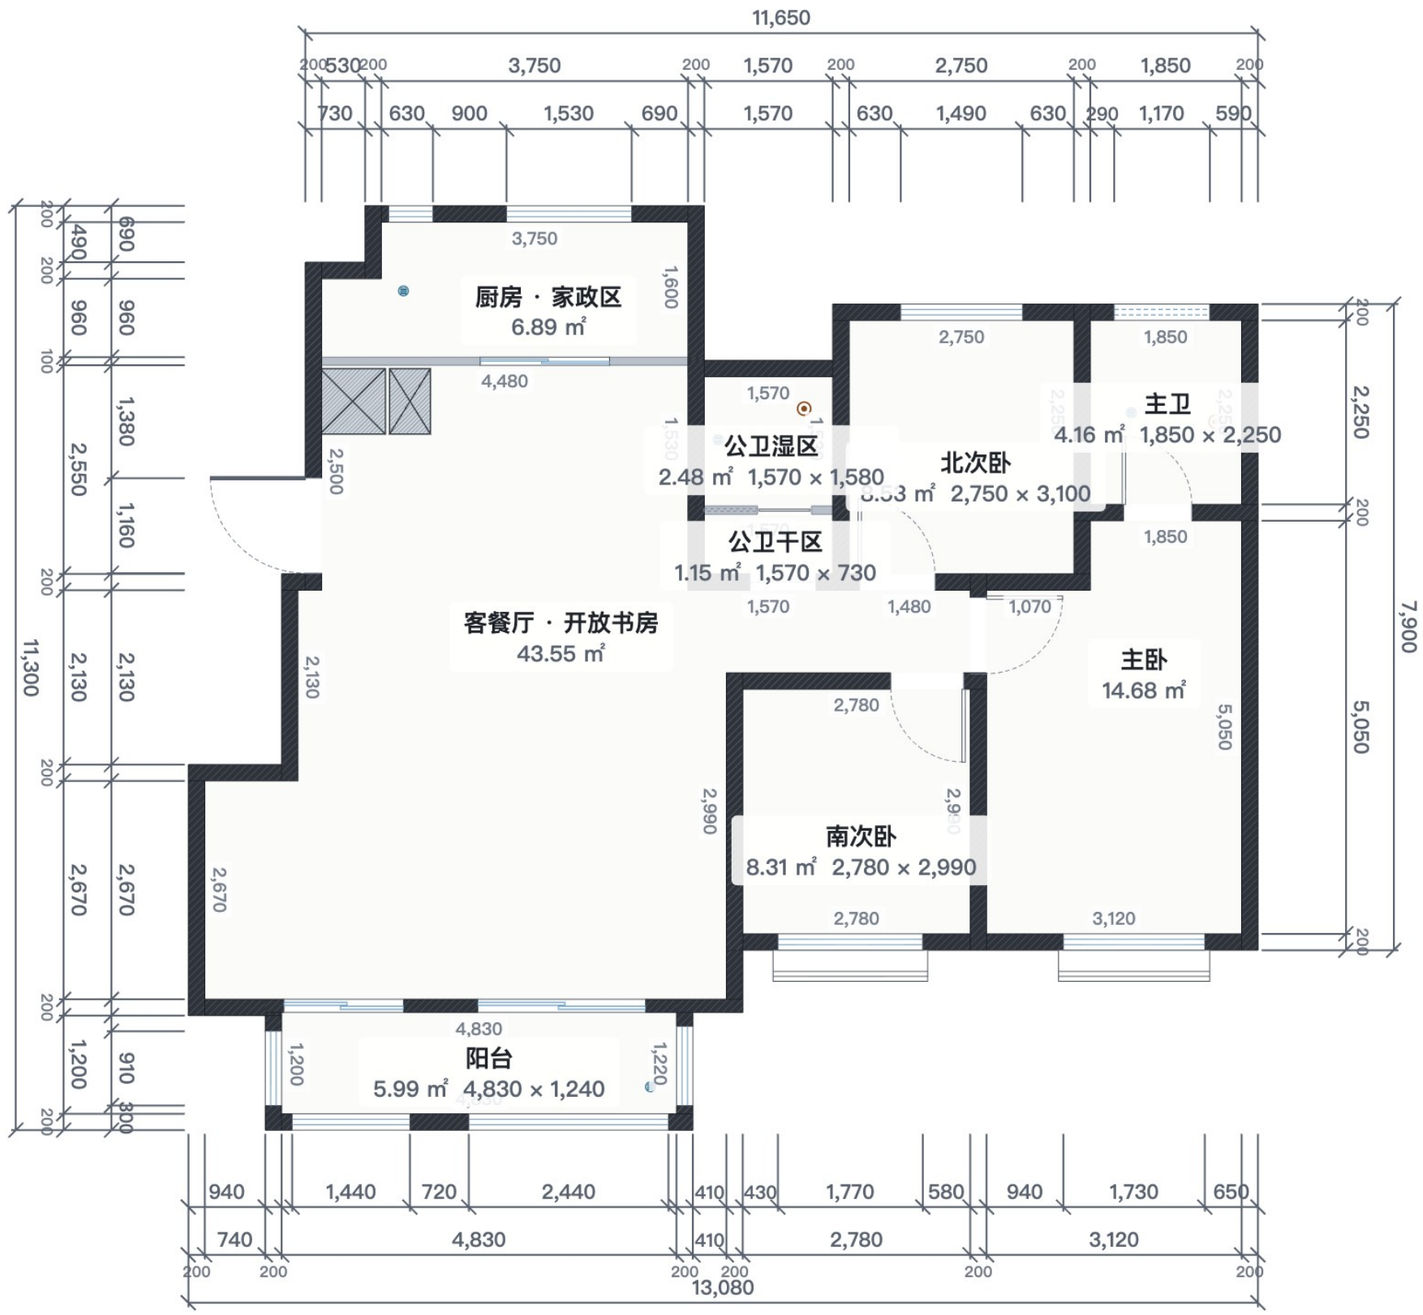


项目名称	比例	单位
D户型128㎡ · 四室两厅两卫	1:75	mm
图名	日期	图号
拆改图	2026/11/10	02 / 32

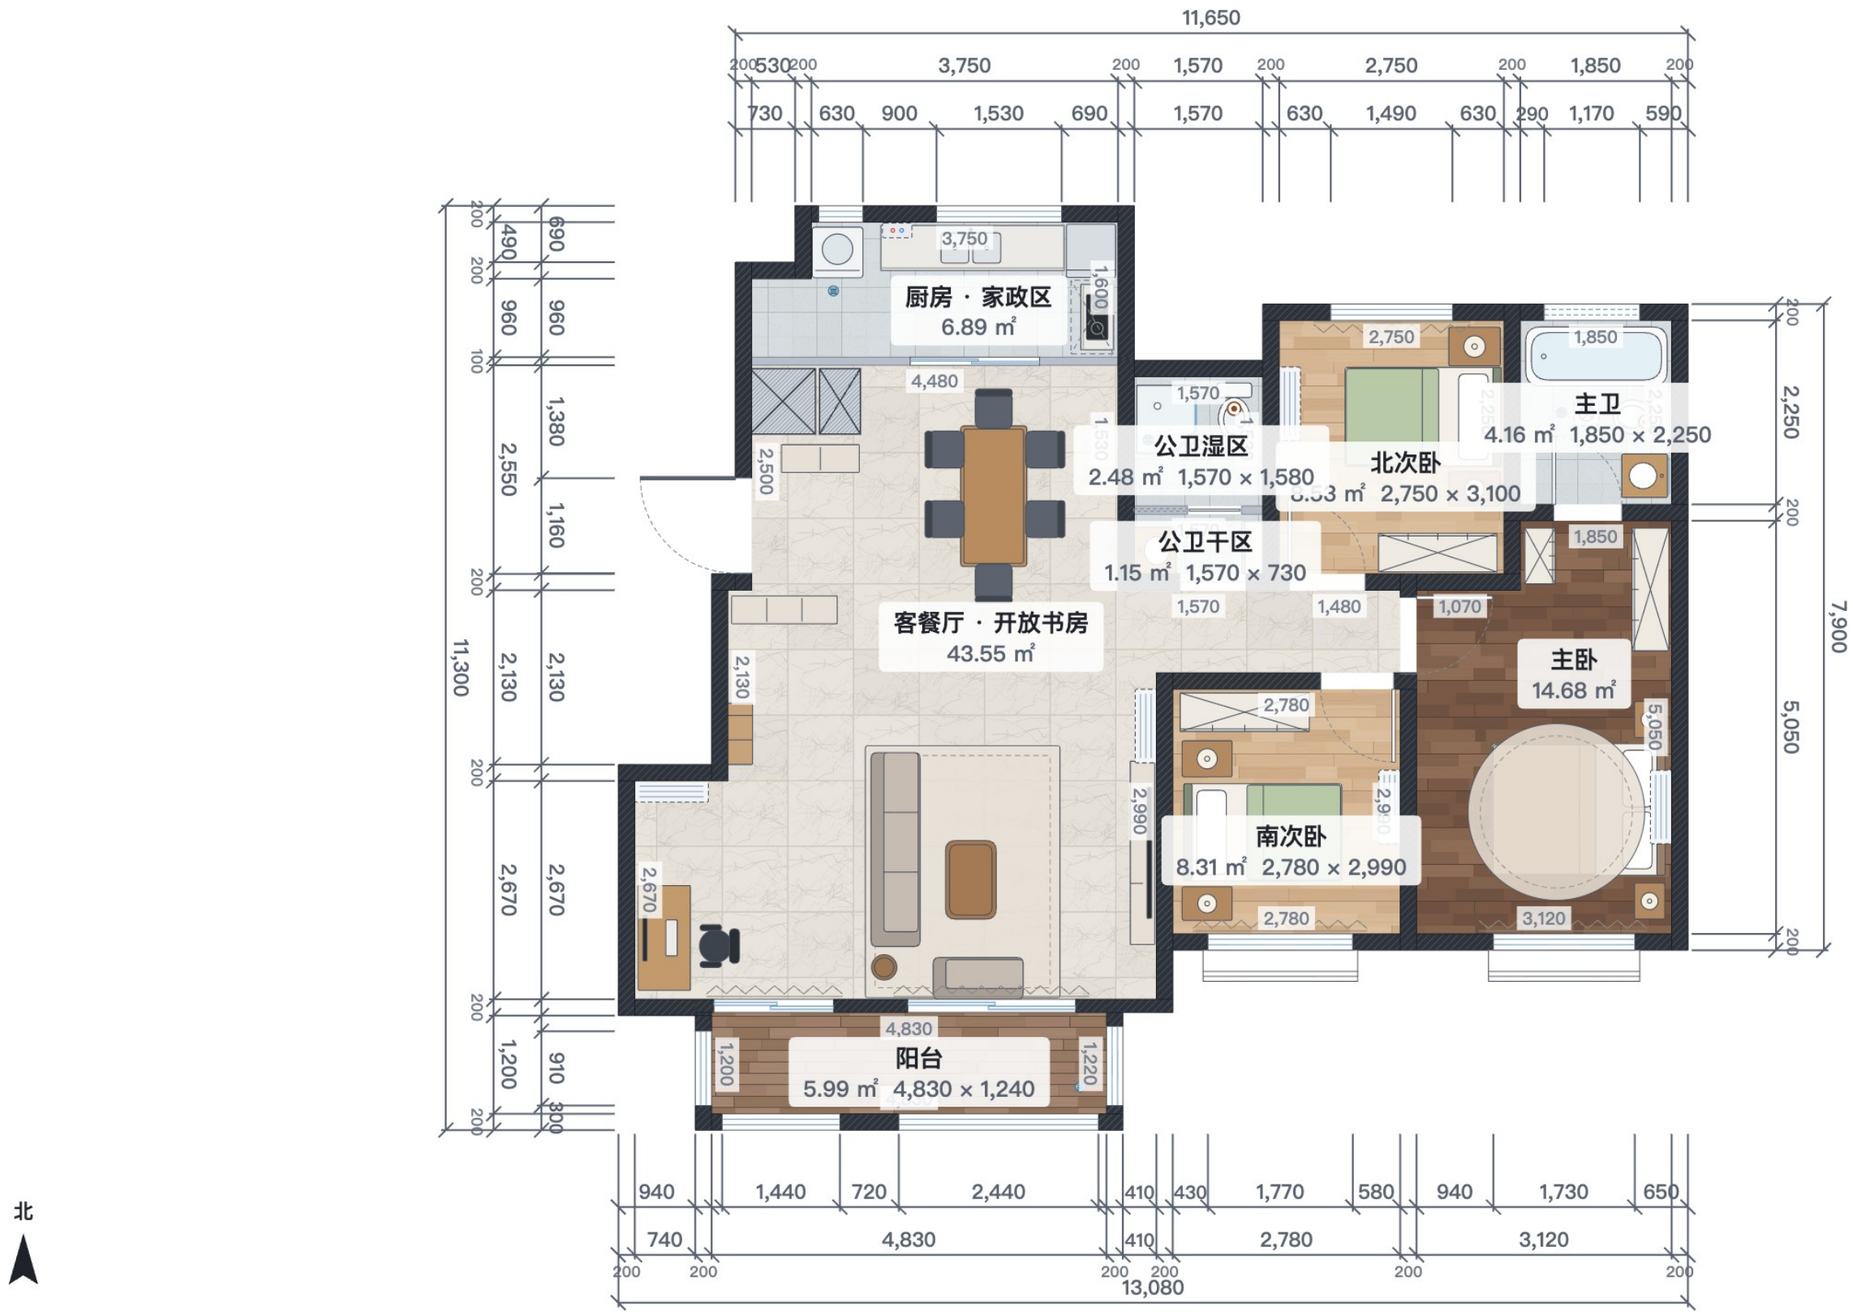


项目名称	比例	单位
D户型128㎡ · 四室两厅两卫	1:75	mm
图名	日期	图号
平面布置图	2026/11/10	03 / 32

防滑砖 300 14.68㎡　橡木地板 16.84㎡　米白大理石 43.55㎡　胡桃木 14.68㎡　户外木塑 5.99㎡

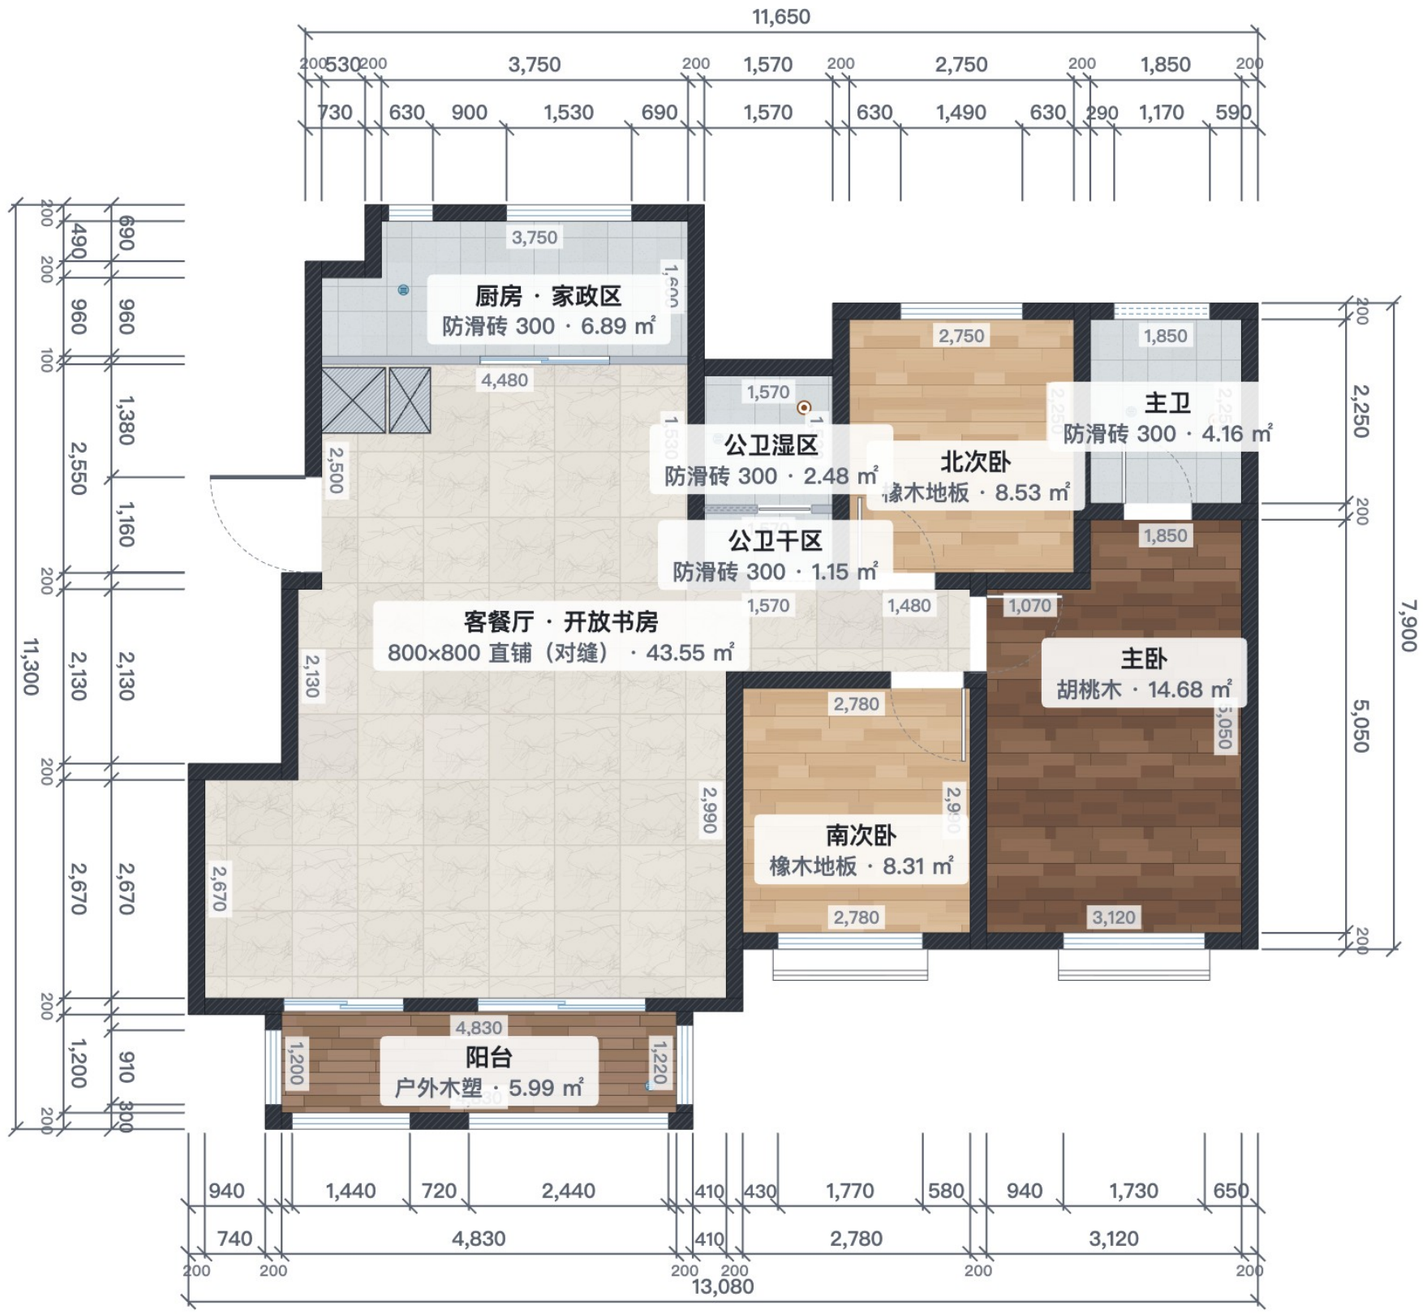

项目名称	比例	单位
D户型128㎡ · 四室两厅两卫	1:75	mm
图名	日期	图号
地面铺装图	2026/11/10	04 / 32

石膏板吊顶　灯槽　主灯　筒灯/射灯　层高 2,800 · 本方案：平顶吊顶、不吊顶（刷漆）

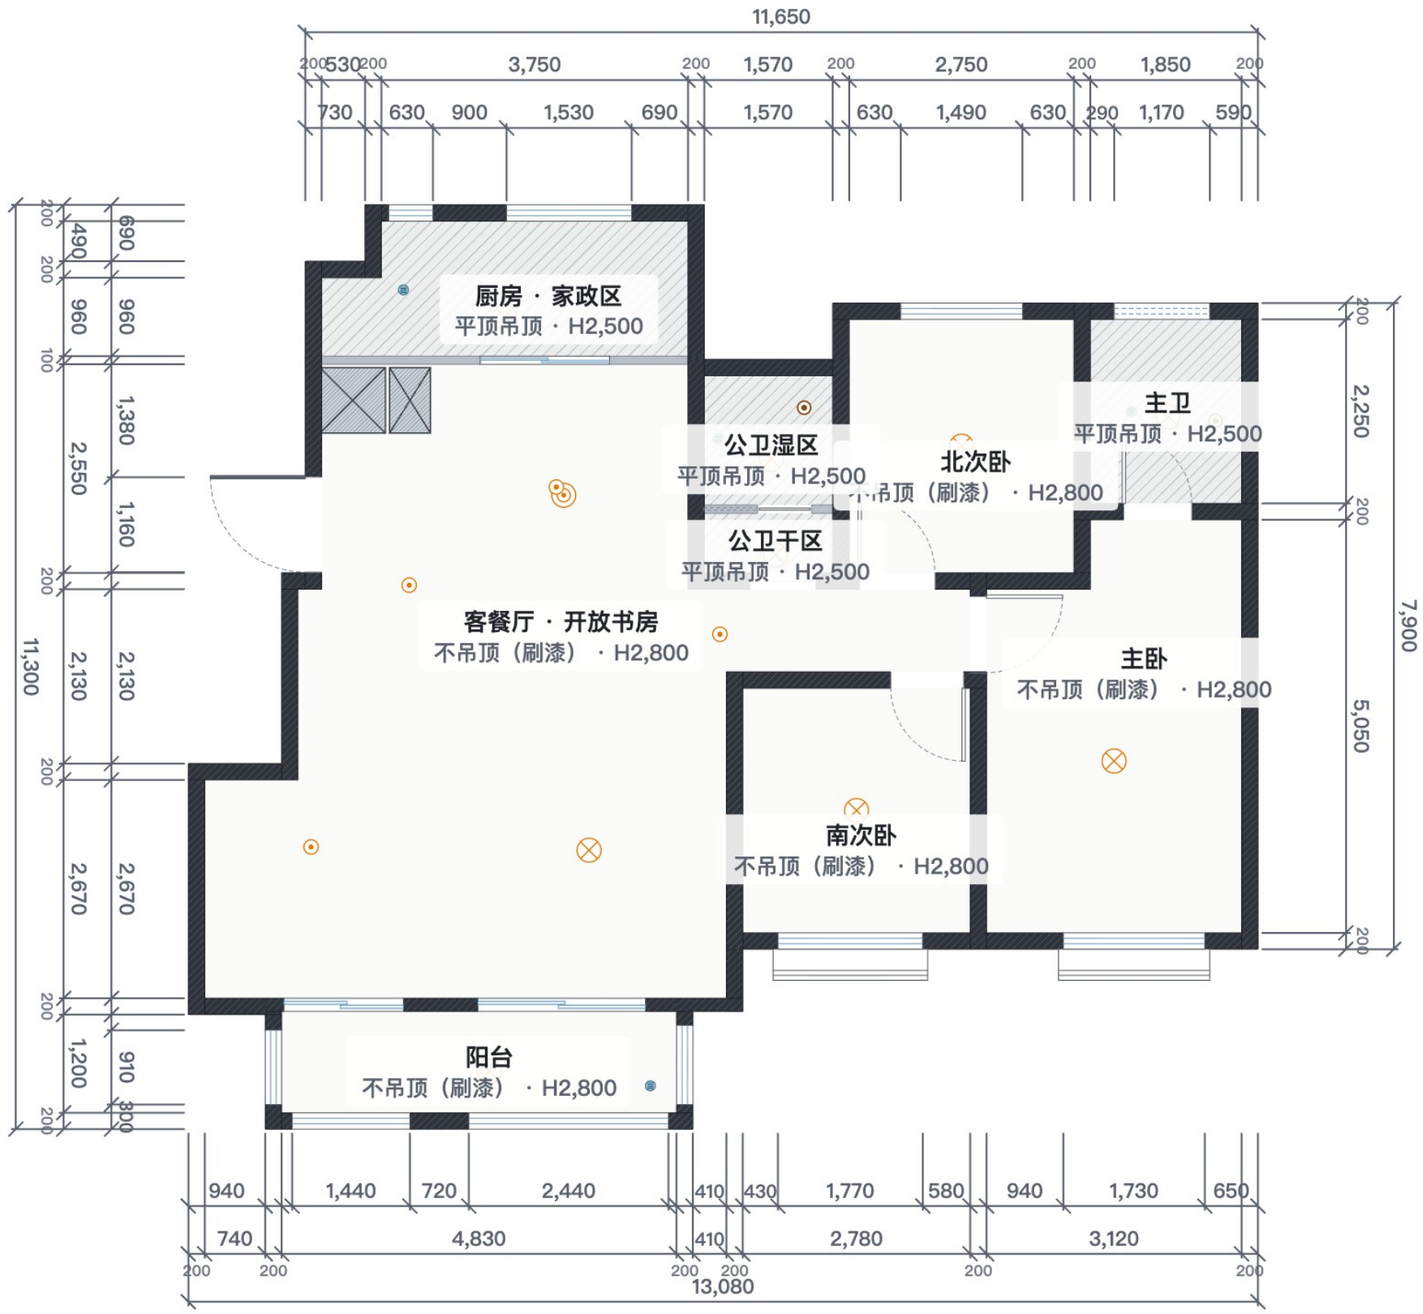


北

2 m

项目名称	比例	单位
D户型128㎡ · 四室两厅两卫	1:75	mm
图名	日期	图号
顶面布置图	2026/11/10	05 / 32

吸顶灯 ×9　烟感 / 燃气报警 ×1　单控开关 ×6　双控开关 ×5　五孔插座 ×24　网络插座 ×5　吊灯 ×1　筒灯 ×4　三开开关 ×1　可视对讲 ×1　强电箱 ×1　弱电箱 ×1　电视插座 ×2
防水插座 ×11　冷水点 ×9　热水点 ×6　墙排水口 ×3　烟机插座 ×1　燃气点 ×2　USB 插座 ×7　地插 ×1　空调插座 ×5　空调孔 ×5　开关控制关系

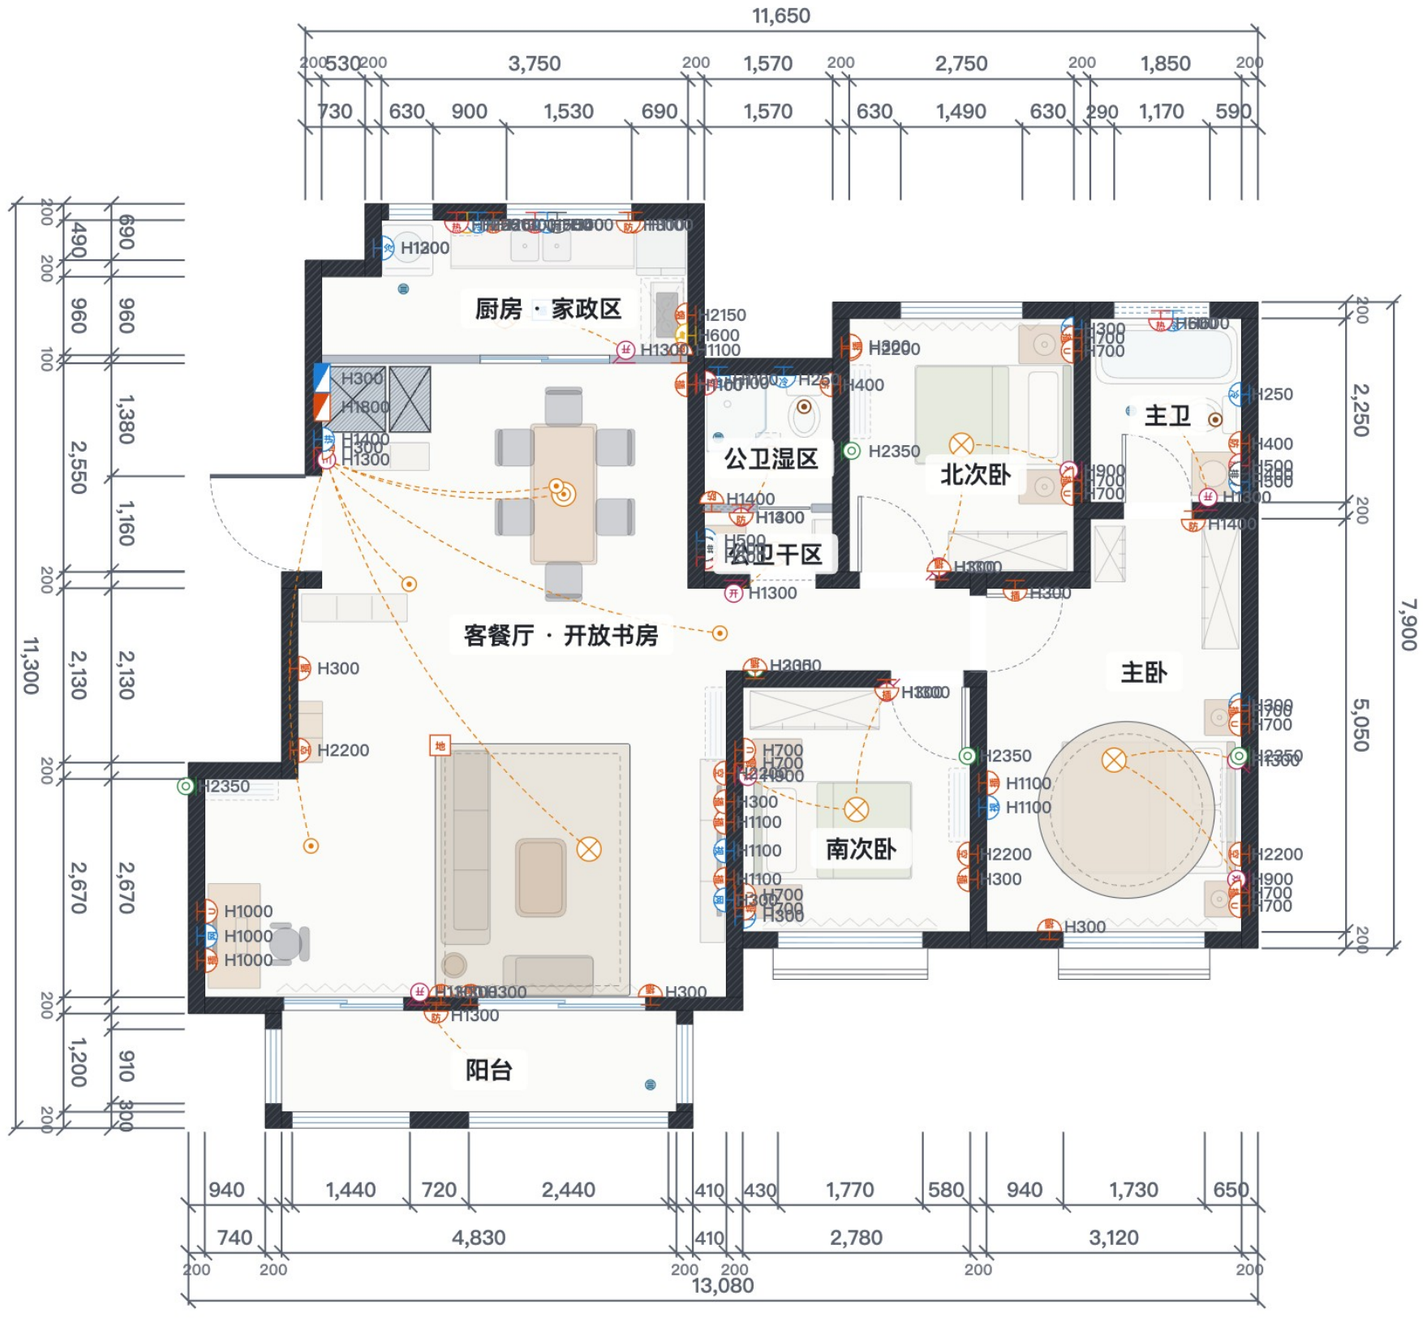


北

2 m


项目名称 D户型128㎡ · 四室两厅两卫	比例 1:75	单位 mm
图名 水电点位图	日期 2026/11/10	图号 06 / 32

插座回路　长虚线 = 走顶　五孔插座 ×24　强电箱 ×1　防水插座 ×11　烟机插座 ×1　USB 插座 ×7　地插 ×1　空调插座 ×5

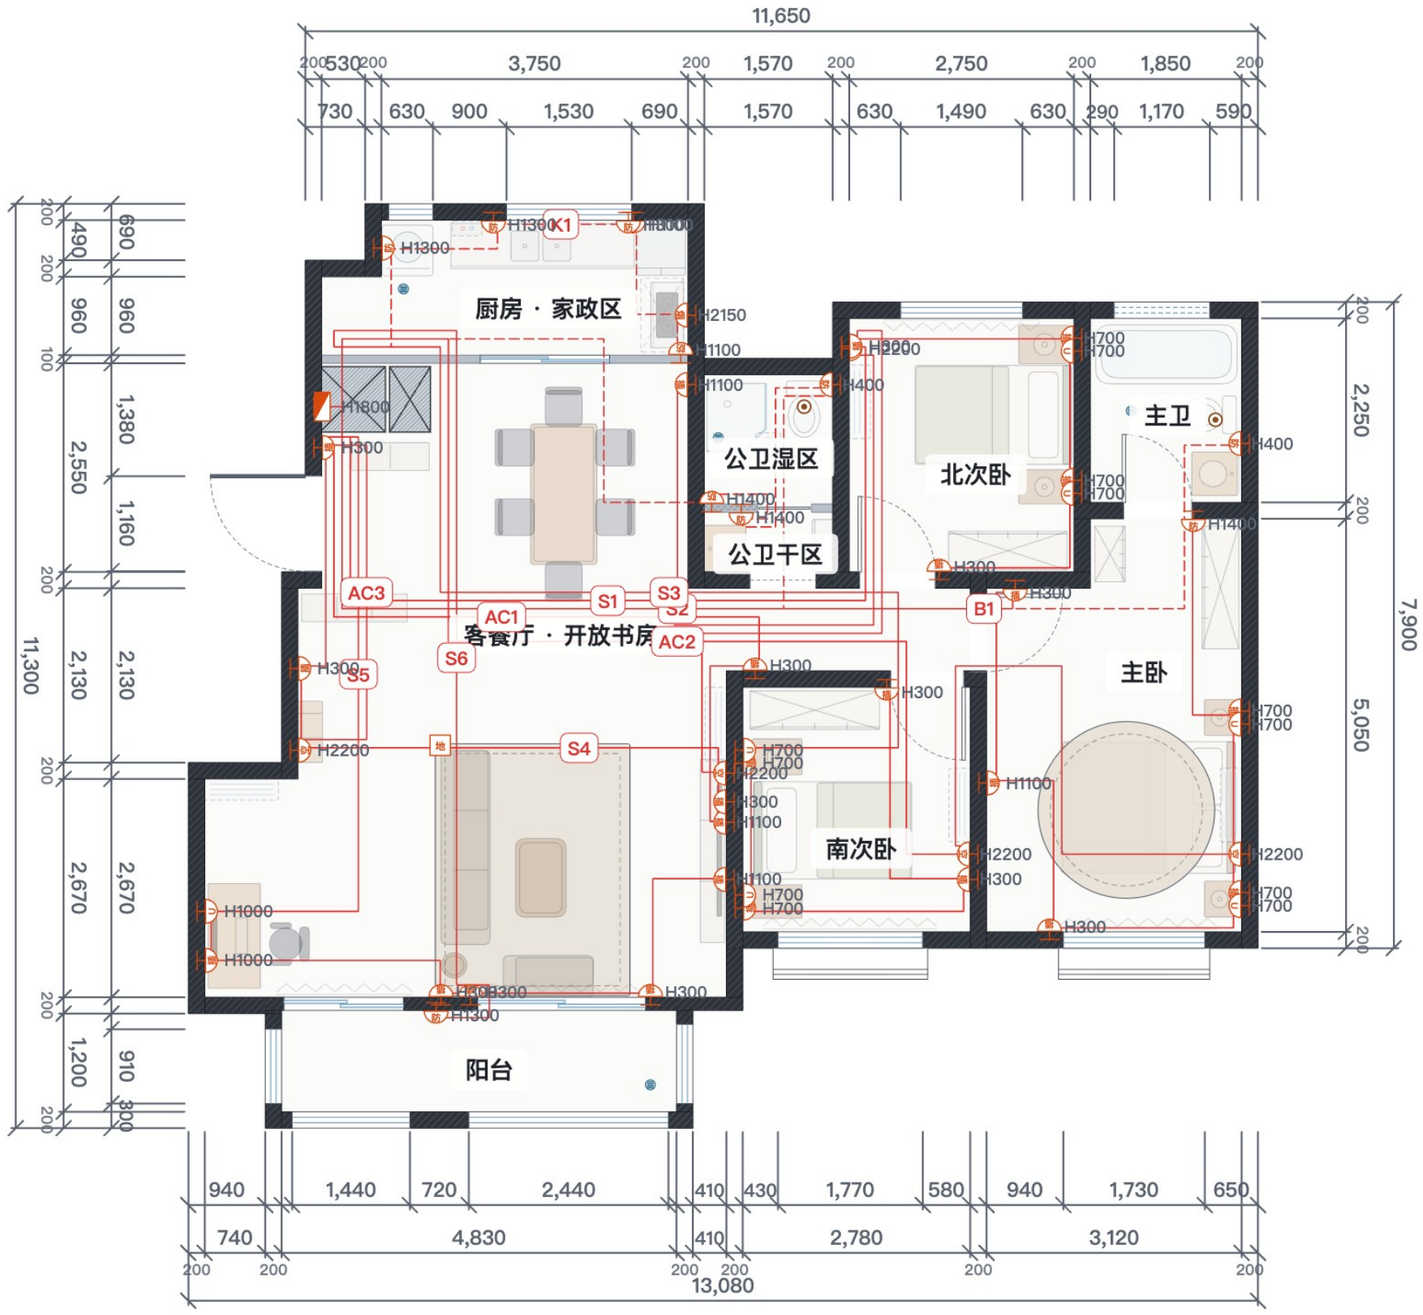

项目名称 D户型128㎡ · 四室两厅两卫	比例 1:75	单位 mm
图名 强电插座线路图	日期 2026/11/10	图号 07 / 32

照明回路　长虚线 = 走顶　吸顶灯 ×9　单控开关 ×6　双控开关 ×5　吊灯 ×1　筒灯 ×4　三开开关 ×1　强电箱 ×1

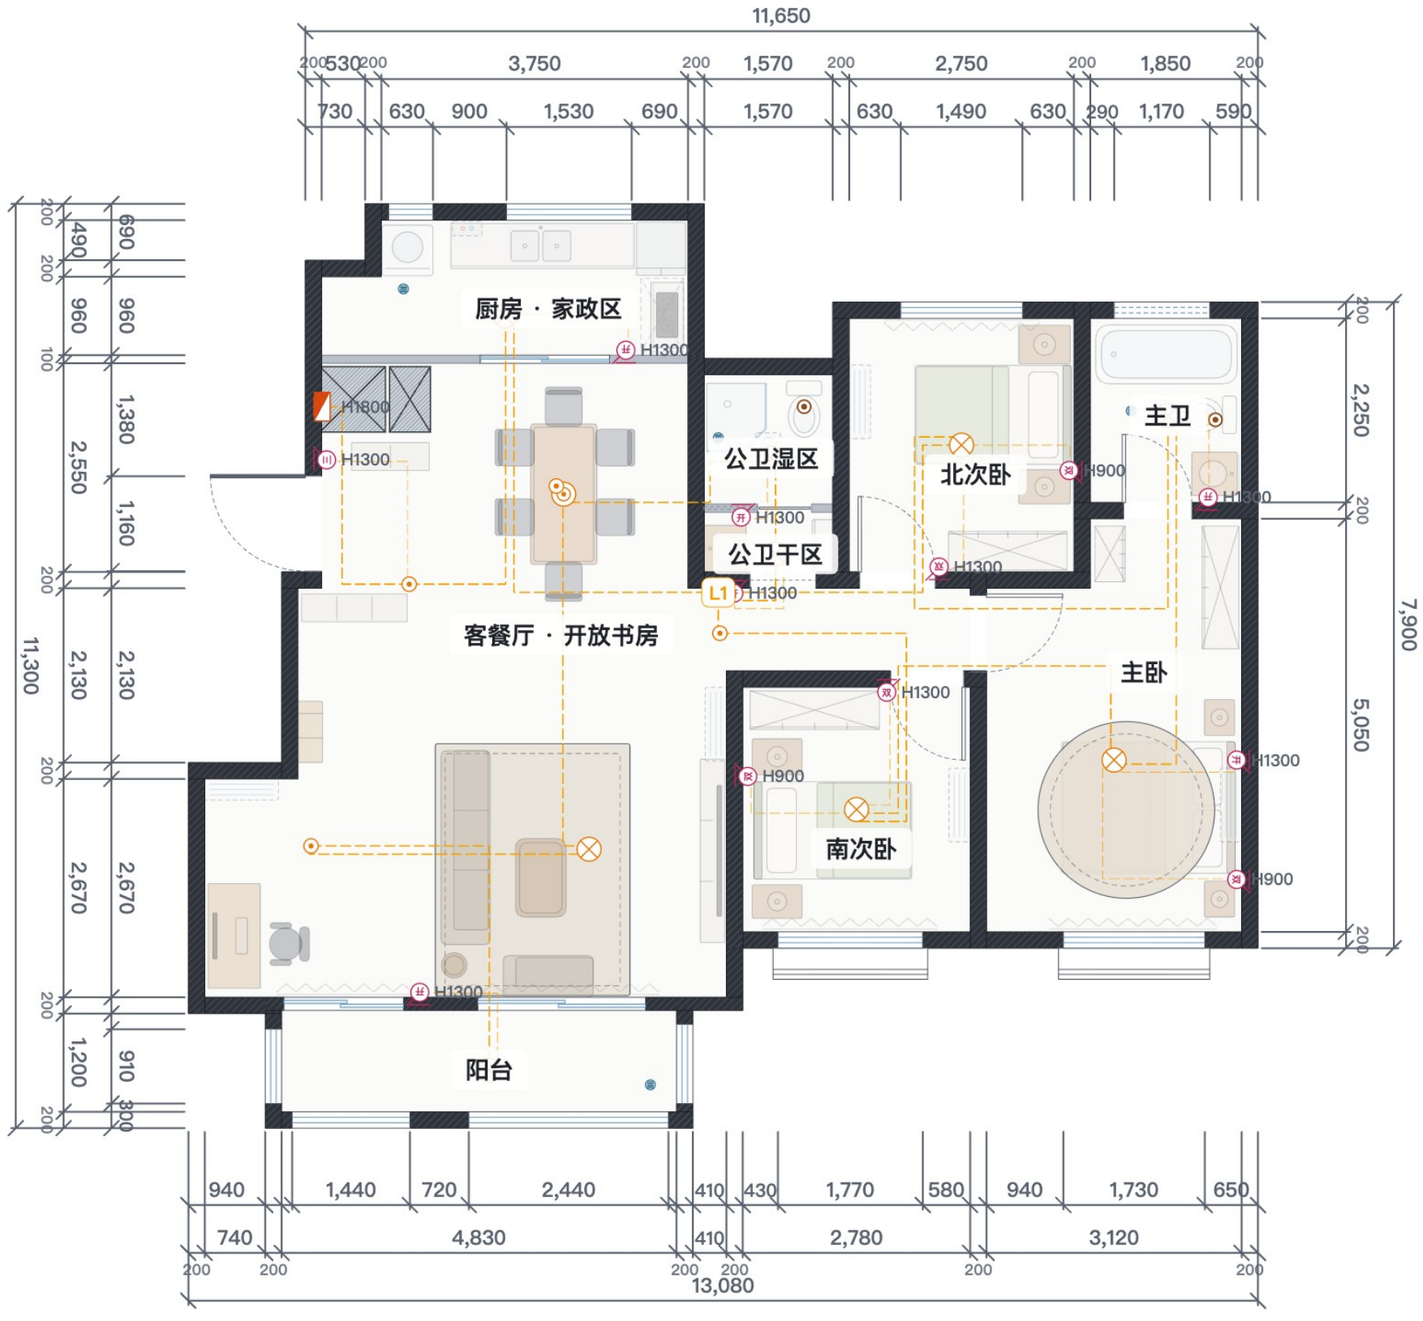


北

2 m


项目名称	比例	单位
D户型128㎡ · 四室两厅两卫	1:75	mm
图名	日期	图号
照明线路图	2026/11/10	08 / 32

弱电（网线）　长虚线 = 走顶　网络插座 ×5　可视对讲 ×1　弱电箱 ×1　电视插座 ×2

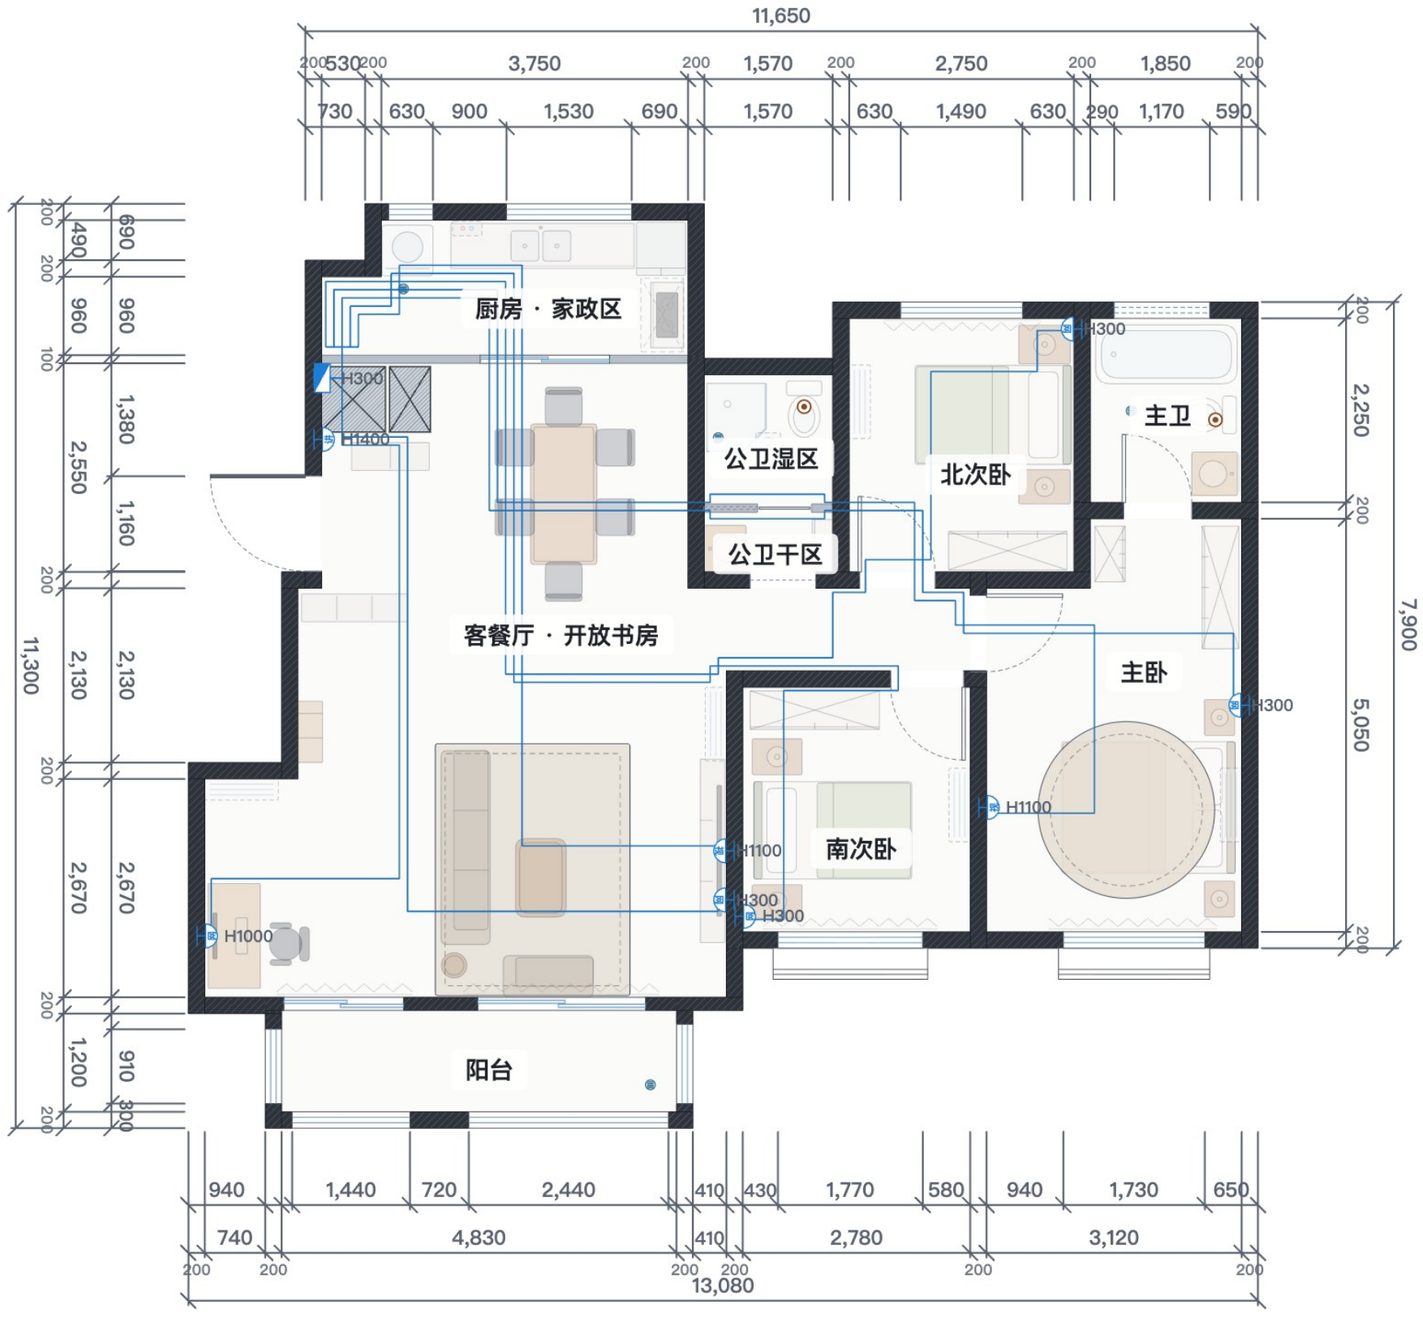


项目名称 D户型128㎡ · 四室两厅两卫	比例 1:75	单位 mm
图名 弱电网线布线图	日期 2026/11/10	图号 09 / 32

冷水管　热水管　长虚线 = 走顶　冷水点 ×9　热水点 ×6

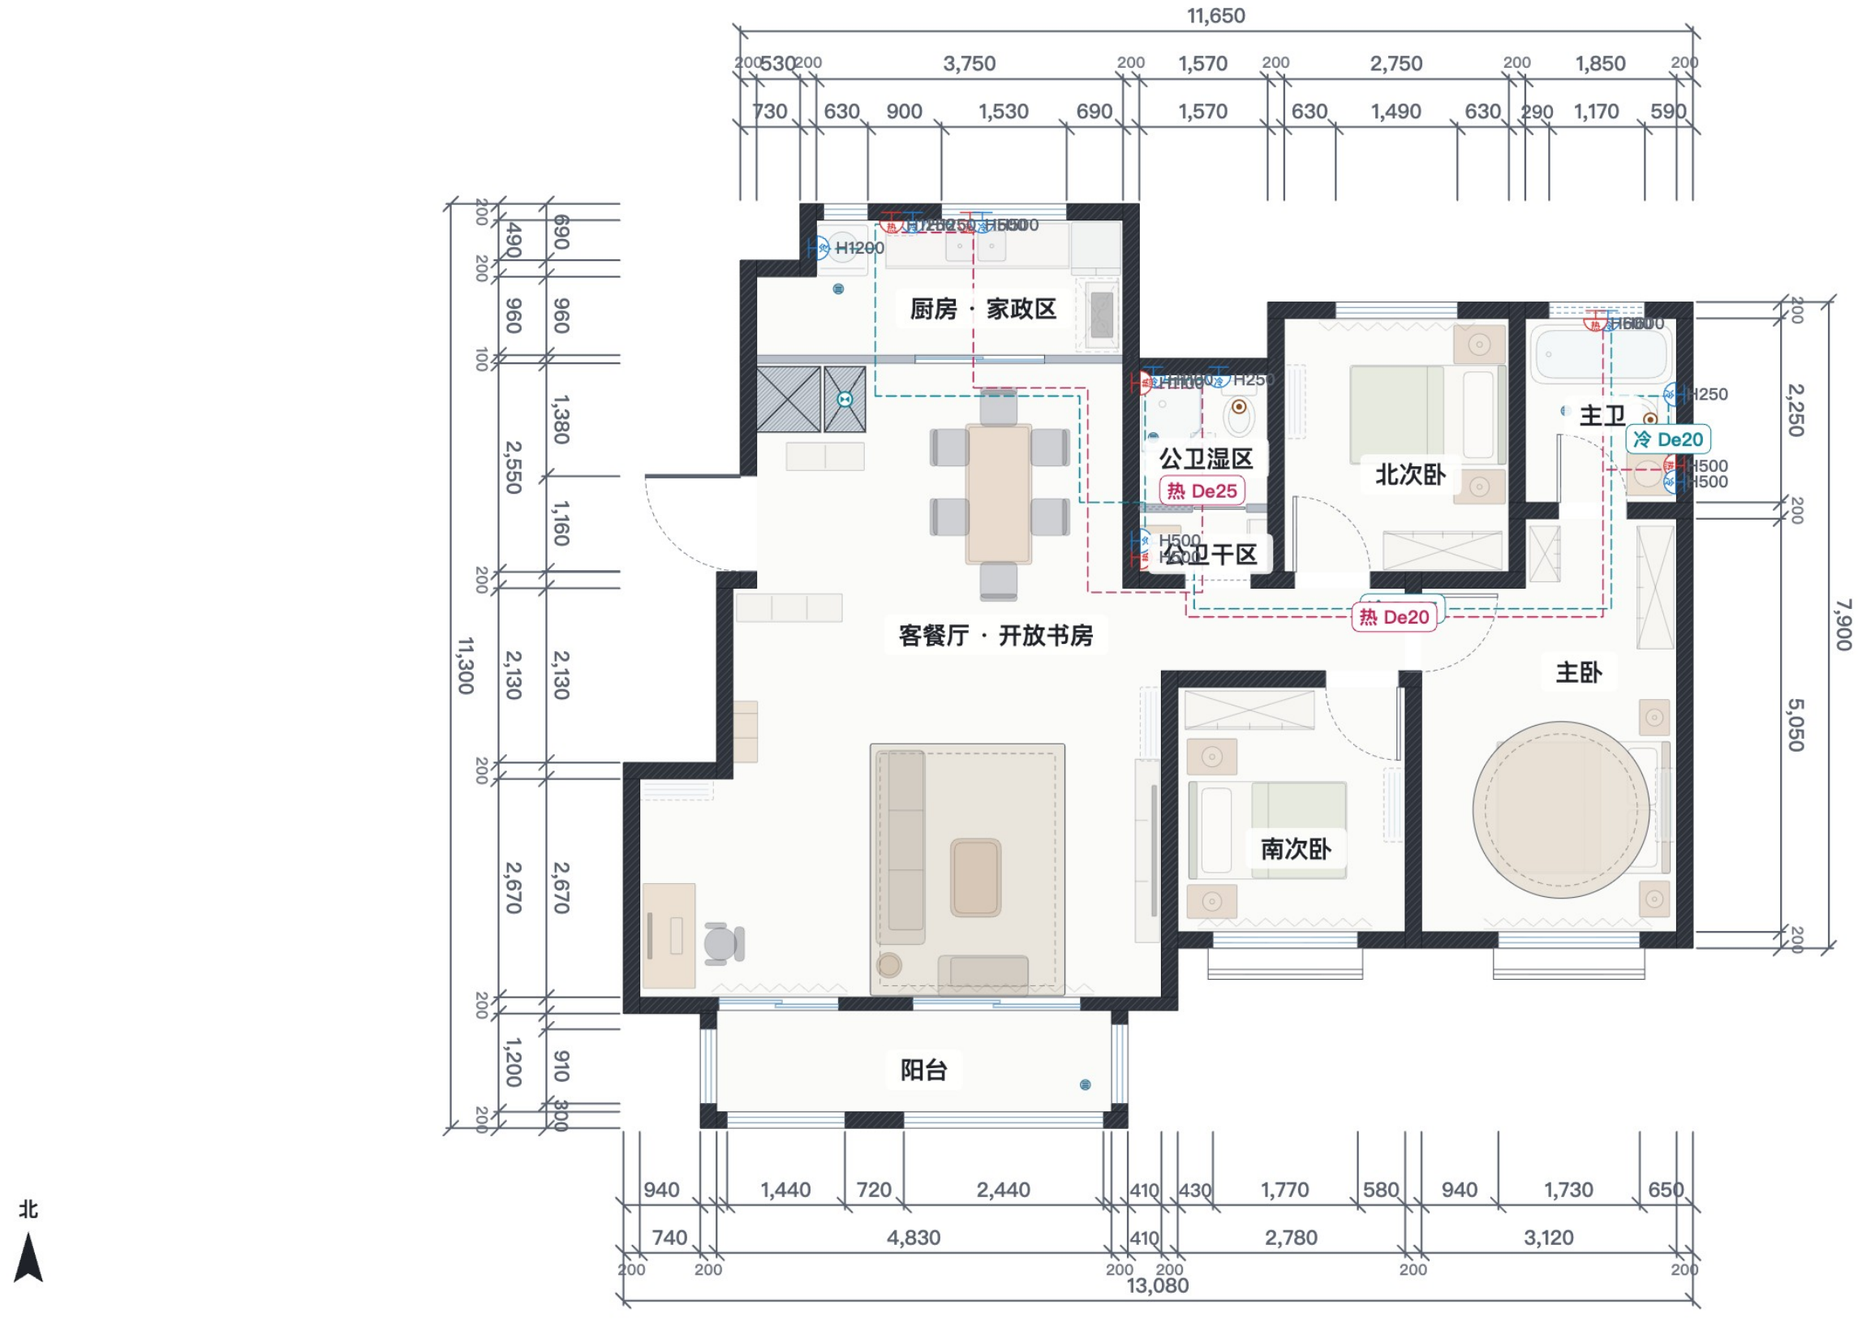

项目名称	比例	单位
D户型128㎡ · 四室两厅两卫	1:75	mm
图名	日期	图号
给水（冷热水）管路图	2026/11/10	10 / 32


排水管　长虚线 = 走顶　墙排水口 ×3

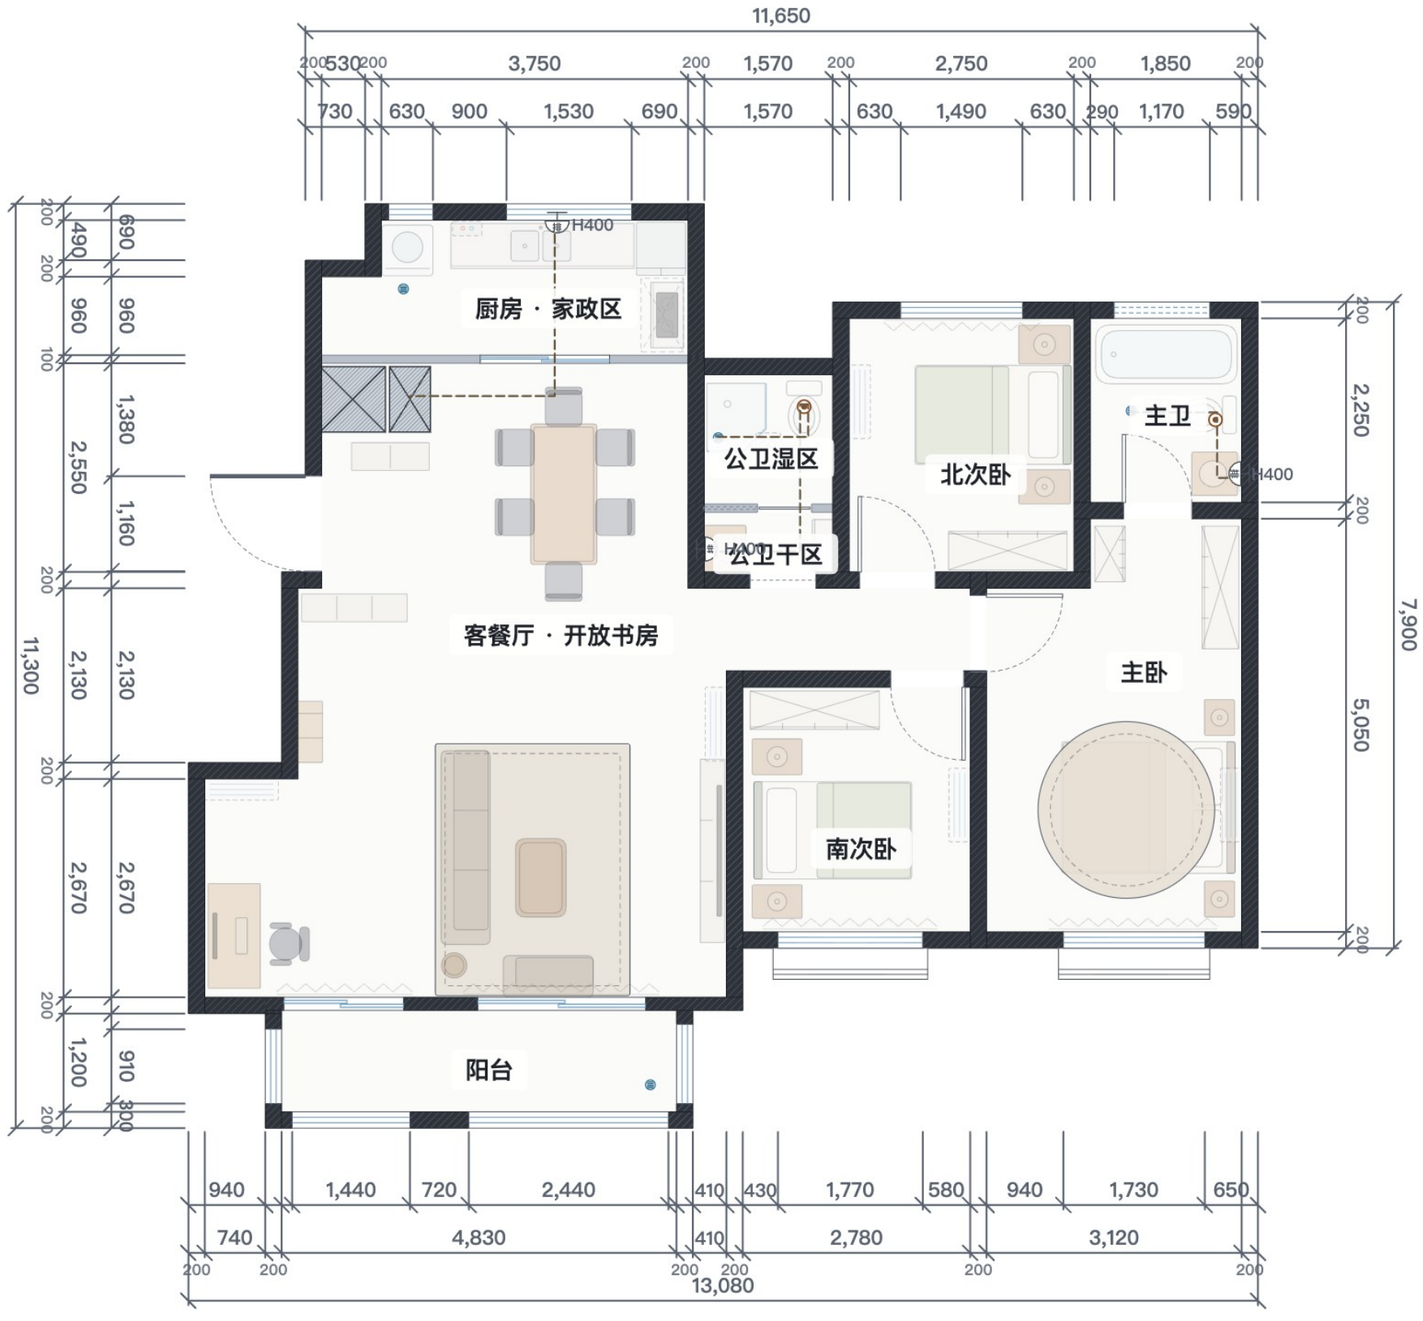

项目名称	比例	单位
D户型128㎡ · 四室两厅两卫	1:75	mm
图名	日期	图号
排水管路图	2026/11/10	11 / 32


厨房 · 家政区 · 北立面

墙面：墙砖 · 踢脚线：无 · 吊顶后净高 2,500 · 净长 3,750 · 单位 mm

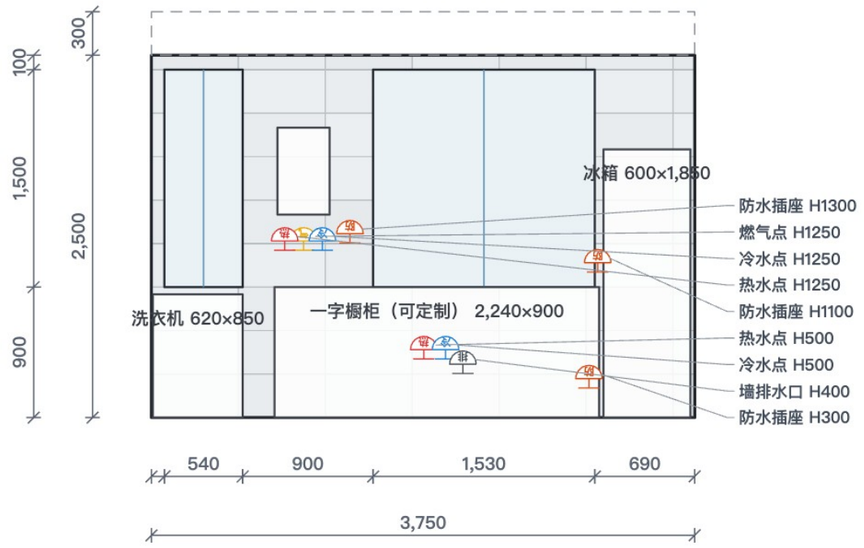

厨房 · 家政区 · 东立面


墙面：墙砖 · 踢脚线：无 · 吊顶后净高 2,500 · 净长 1,600 · 单位 mm

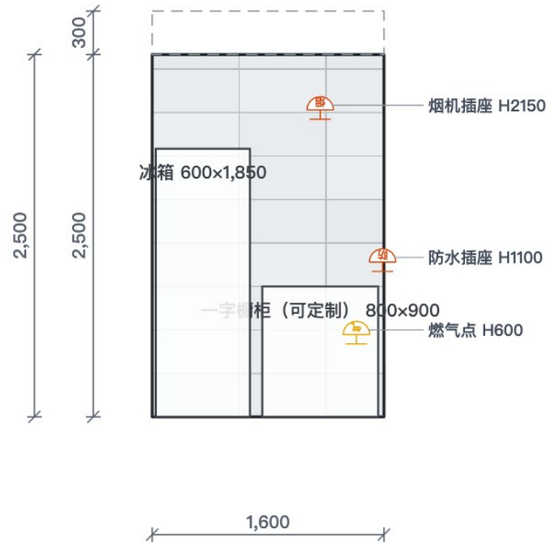

项目名称	比例	单位
D户型128㎡ · 四室两厅两卫	见尺寸	mm
图名：立面图 · 厨房 · 家政区 · 北立面 / 厨房 · 家政区 · 东立面	日期：2026/11/10	图号：12 / 32


公卫湿区 · 北立面

墙面：墙砖 · 踢脚线：无 · 吊顶后净高 2,500 · 净长 1,570 · 单位 mm

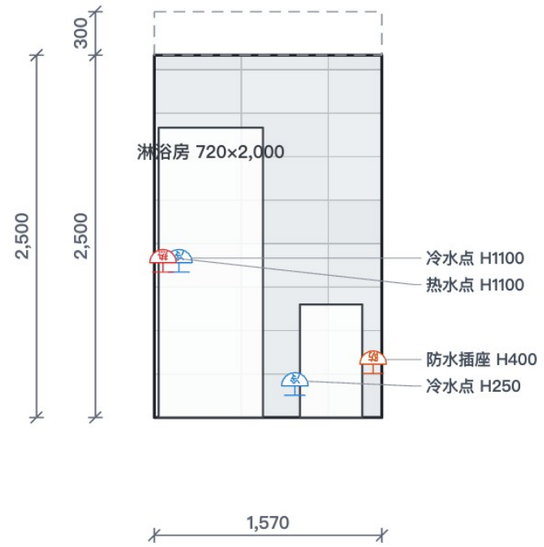

北次卧 · 西立面


墙面：奶咖乳胶漆 · 踢脚线：实木 80 · 吊顶后净高 2,800 · 净长 3,100 · 单位 mm

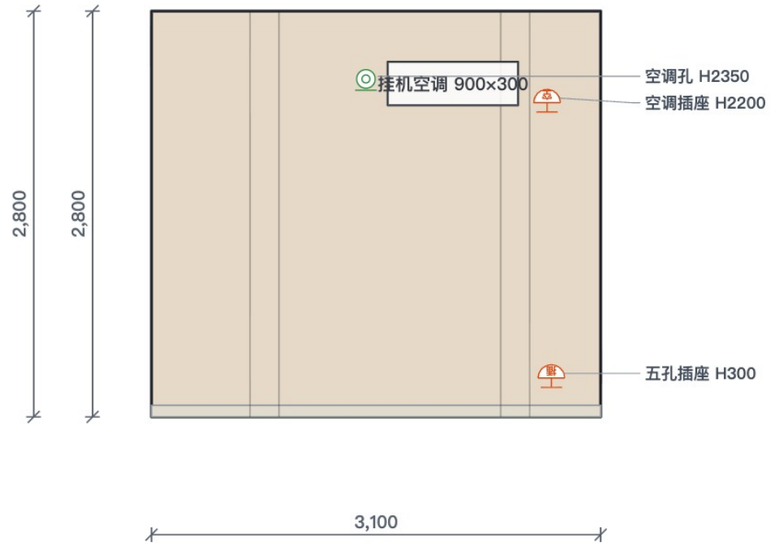

项目名称 D户型128㎡ · 四室两厅两卫		比例 见尺寸	单位 mm
图名 立面图 · 公卫湿区 · 北立面 / 北次卧 · 西立面		日期 2026/11/10	图号 13 / 32


北次卧 · 北立面

墙面：奶咖乳胶漆 · 踢脚线：实木 80 · 吊顶后净高 2,800 · 净长 2,750 · 单位 mm

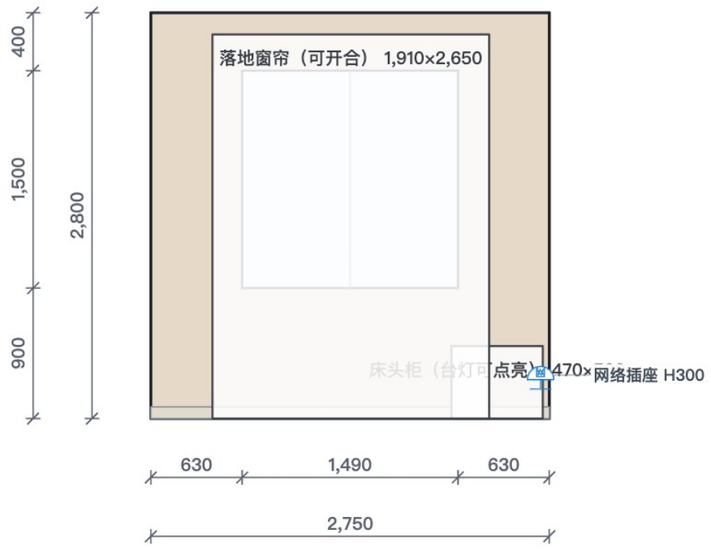

主卫 · 东立面


墙面：墙砖 · 踢脚线：无 · 吊顶后净高 2,500 · 净长 2,250 · 单位 mm

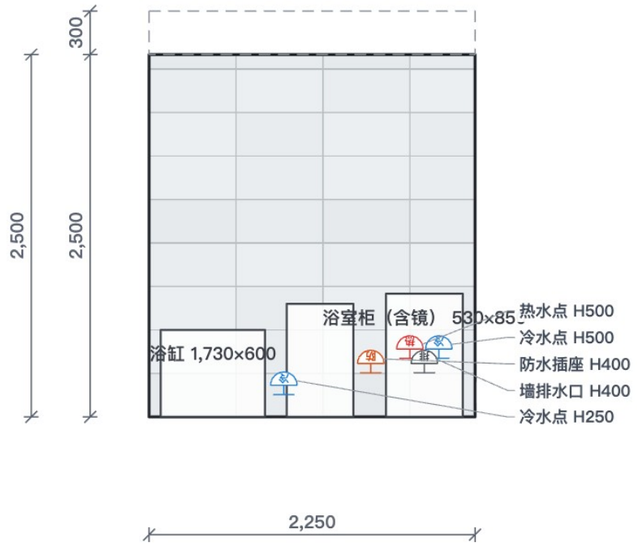

项目名称	比例	单位
D户型128㎡ · 四室两厅两卫	见尺寸	mm
图名	日期	图号
立面图 · 北次卧 · 北立面 / 主卫 · 东立面	2026/11/10	14 / 32


主卧 · 南立面

墙面：奶咖乳胶漆 · 踢脚线：实木 80 · 吊顶后净高 2,800 · 净长 3,120 · 单位 mm

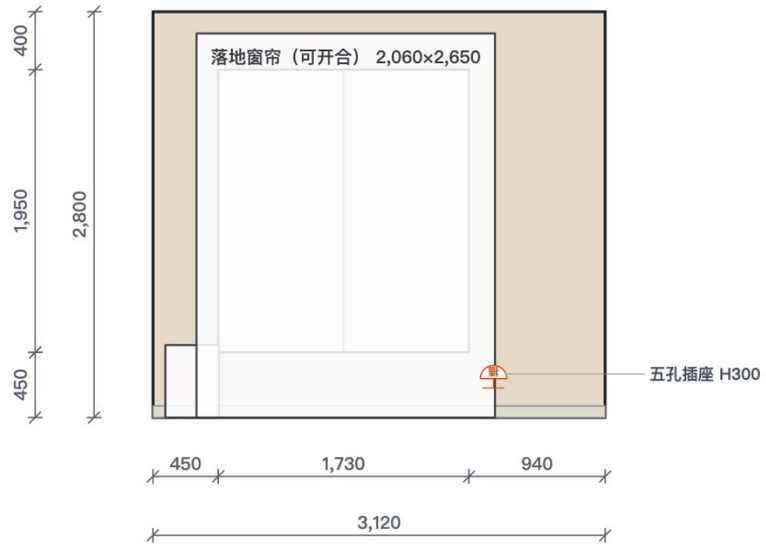

客餐厅 · 开放书房 · 东立面


墙面：奶咖乳胶漆 · 踢脚线：实木 80 · 吊顶后净高 2,800 · 净长 3,810 · 单位 mm

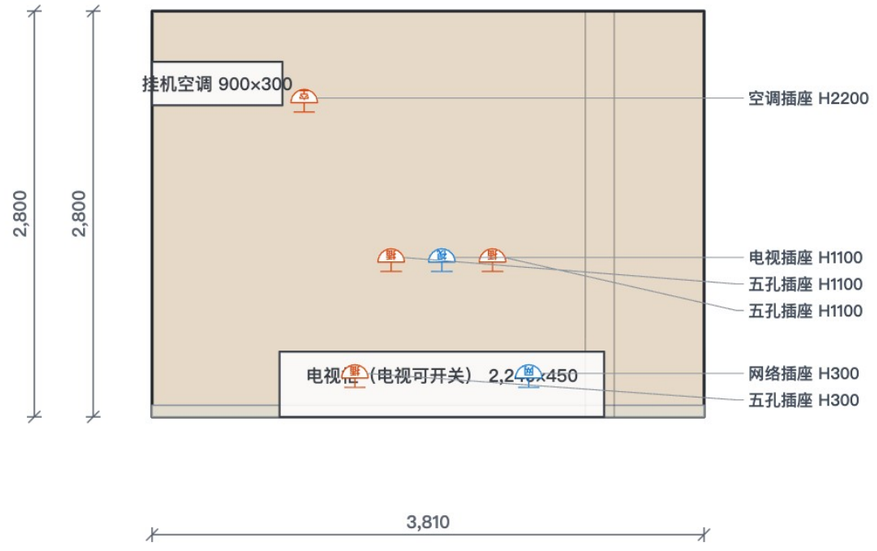

项目名称	比例	单位
D户型128㎡ · 四室两厅两卫	见尺寸	mm
图名	日期	图号
立面图 · 主卧 · 南立面 / 客餐厅 · 开放书房 · 东立面	2026/11/10	15 / 32


客餐厅 · 开放书房 · 南立面

墙面：奶咖乳胶漆 · 踢脚线：实木 80 · 吊顶后净高 2,800 · 净长 6,380 · 单位 mm

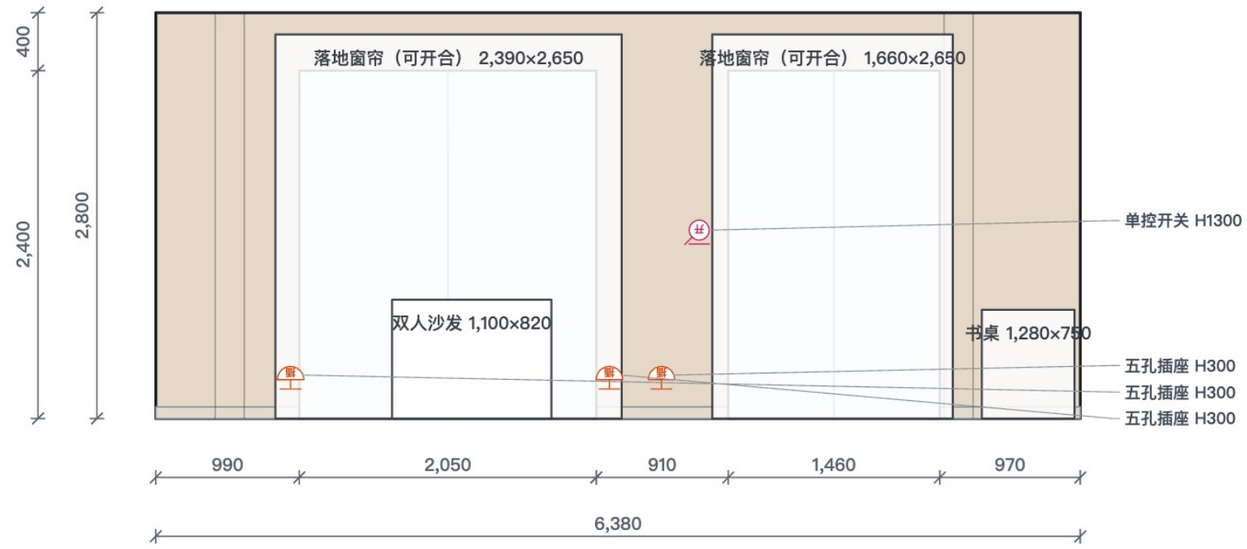

客餐厅 · 开放书房 · 西立面


墙面：奶咖乳胶漆 · 踢脚线：实木 80 · 吊顶后净高 2,800 · 净长 2,670 · 单位 mm

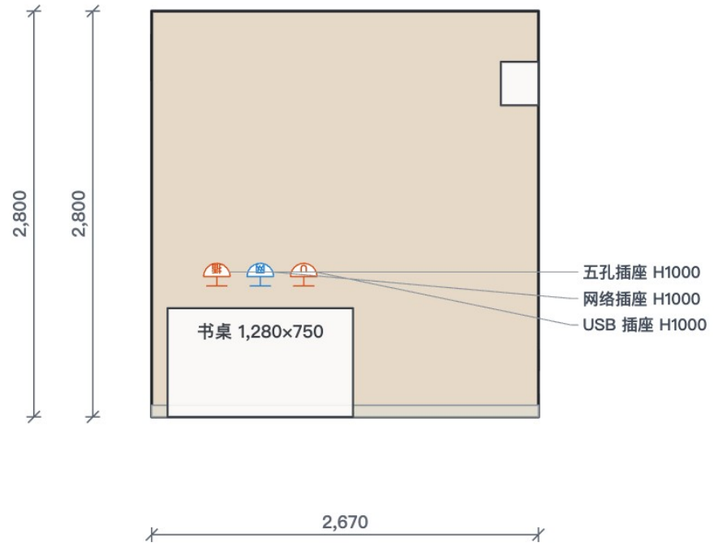

项目名称	比例	单位
D户型128㎡ · 四室两厅两卫	见尺寸	mm
图名：立面图 · 客餐厅 · 开放书房 · 南立面 / 客餐厅 · 开放书房 · 西立面	日期：2026/11/10	图号：16 / 32


客餐厅 · 开放书房 · 北立面

墙面：奶咖乳胶漆 · 踢脚线：实木 80 · 吊顶后净高 2,800 · 净长 940 · 单位 mm

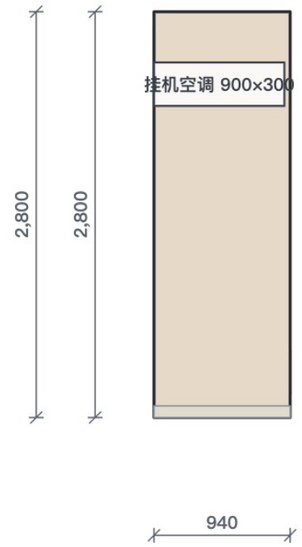

客餐厅 · 开放书房 · 西立面


墙面：奶咖乳胶漆 · 踢脚线：实木 80 · 吊顶后净高 2,800 · 净长 2,130 · 单位 mm

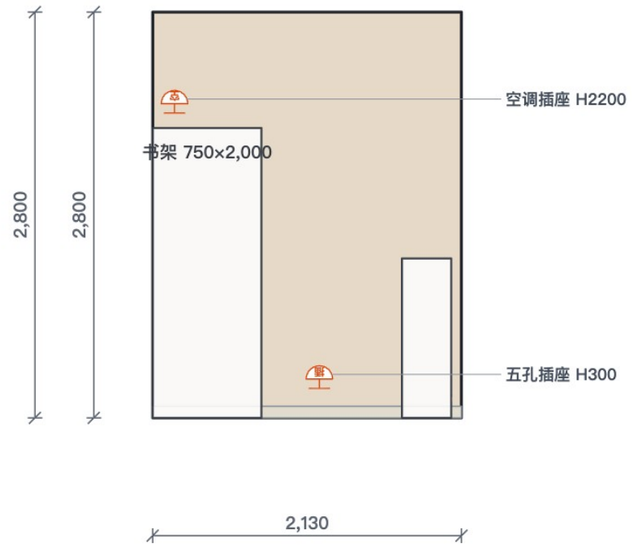

项目名称	比例	单位
D户型128㎡ · 四室两厅两卫	见尺寸	mm
图名：立面图 · 客餐厅 · 开放书房 · 北立面 / 客餐厅 · 开放书房 · 西立面	日期：2026/11/10	图号：17 / 32


客餐厅 · 开放书房 · 北立面

墙面：奶咖乳胶漆 · 踢脚线：实木 80 · 吊顶后净高 2,800 · 净长 8,220 · 单位 mm

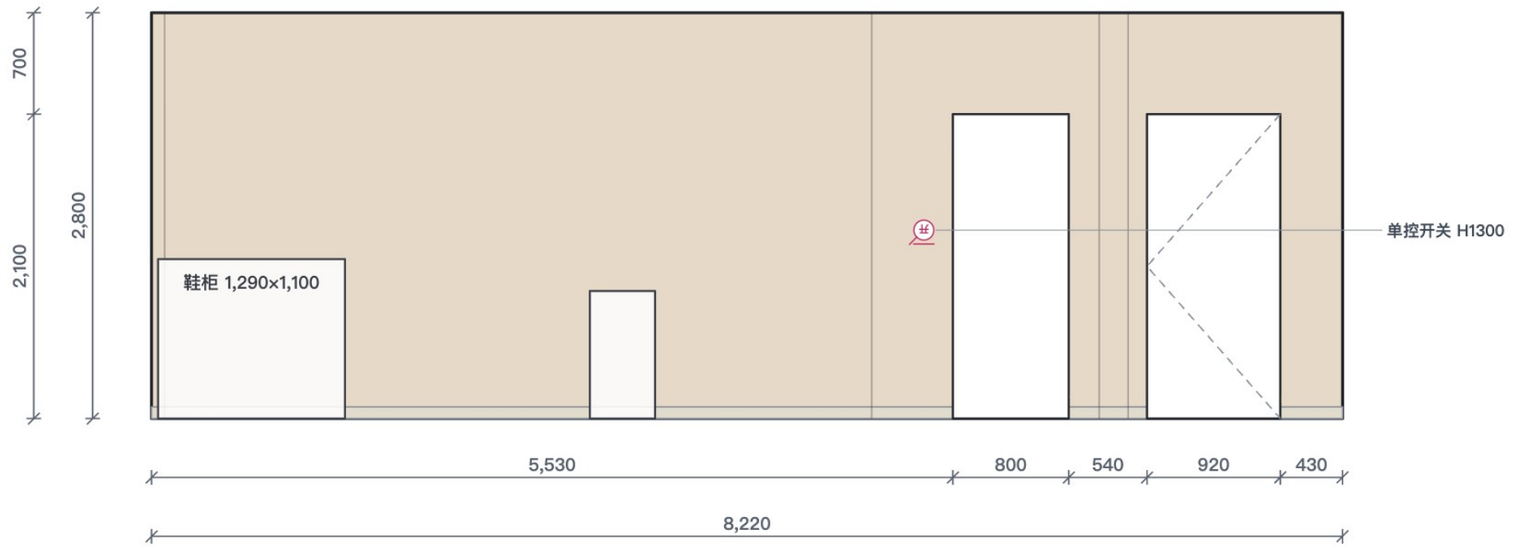

客餐厅 · 开放书房 · 西立面


墙面：奶咖乳胶漆 · 踢脚线：实木 80 · 吊顶后净高 2,800 · 净长 2,500 · 单位 mm

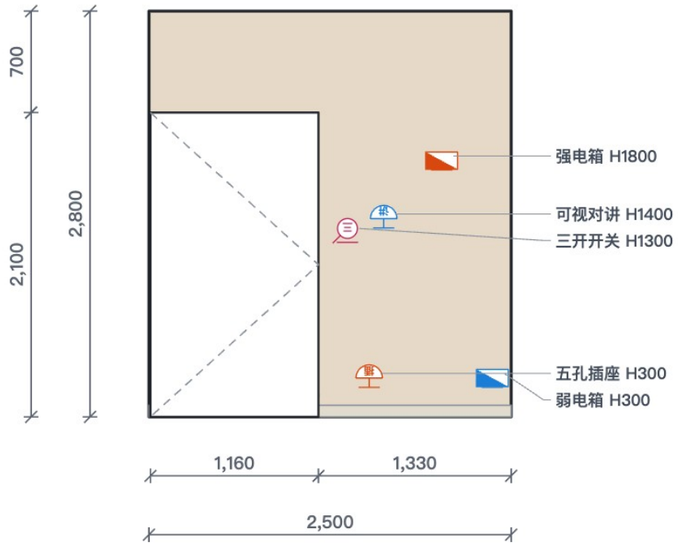

项目名称	比例	单位
D户型128㎡ · 四室两厅两卫	见尺寸	mm
图名：立面图 · 客餐厅 · 开放书房 · 北立面 / 客餐厅 · 开放书房 · 西立面	日期：2026/11/10	图号：18 / 32


厨房 · 家政区 · 西立面

墙面：墙砖 · 踢脚线：无 · 吊顶后净高 2,500 · 净长 910 · 单位 mm

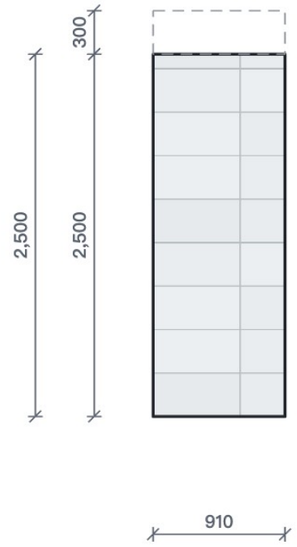

厨房 · 家政区 · 南立面


墙面：墙砖 · 踢脚线：无 · 吊顶后净高 2,500 · 净长 4,480 · 单位 mm

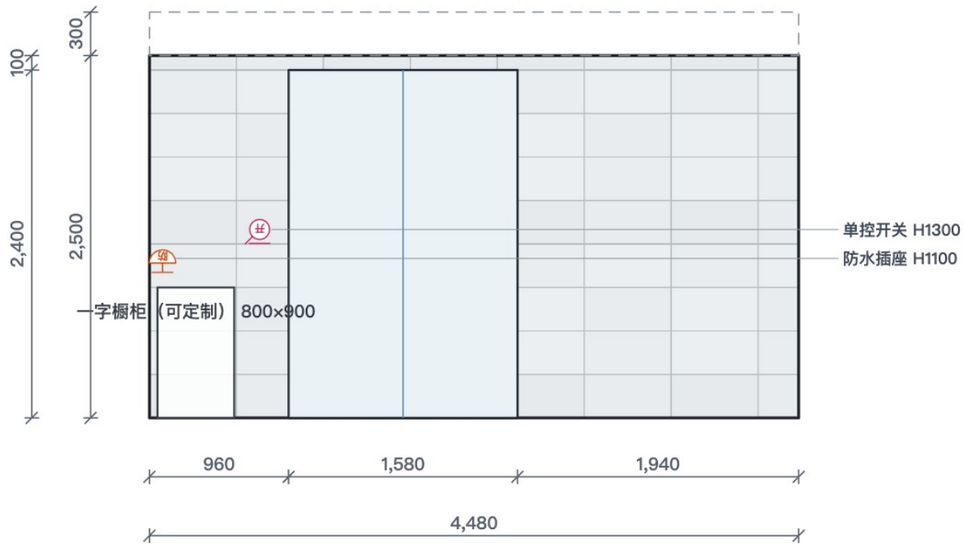

项目名称	比例	单位
D户型128㎡ · 四室两厅两卫	见尺寸	mm
图名：立面图 · 厨房 · 家政区 · 西立面 / 厨房 · 家政区 · 南立面	日期：2026/11/10	图号：19 / 32


客餐厅 · 开放书房 · 东立面

墙面：奶咖乳胶漆 · 踢脚线：实木 80 · 吊顶后净高 2,800 · 净长 2,410 · 单位 mm

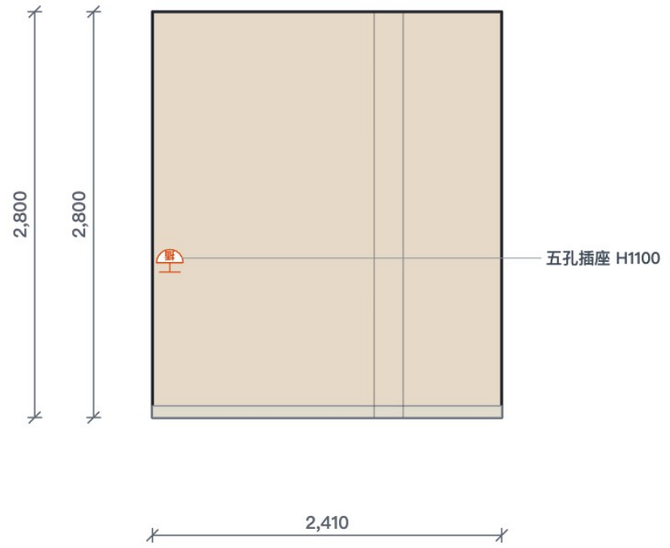

公卫湿区 · 西立面


墙面：墙砖 · 踢脚线：无 · 吊顶后净高 2,500 · 净长 1,530 · 单位 mm

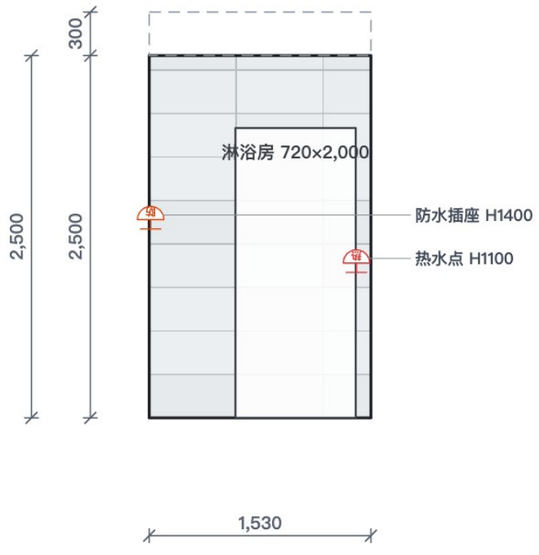

项目名称	比例	单位
D户型128㎡ · 四室两厅两卫	见尺寸	mm
图名 立面图 · 客餐厅 · 开放书房 · 东立面 / 公卫湿区 · 西立面	日期 2026/11/10	图号 20 / 32


公卫干区 · 南立面

墙面：墙砖 · 踢脚线：无 · 吊顶后净高 2,500 · 净长 1,570 · 单位 mm

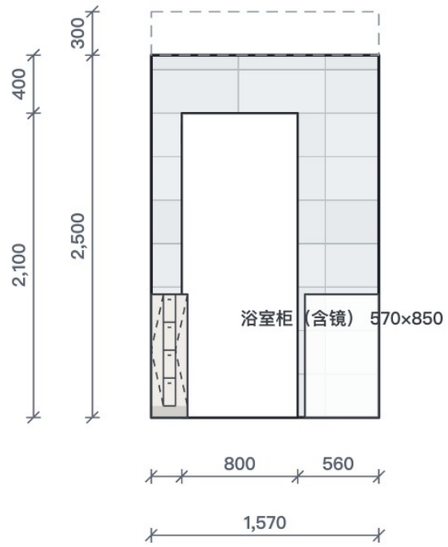

公卫湿区 · 东立面


墙面：墙砖 · 踢脚线：无 · 吊顶后净高 2,500 · 净长 1,530 · 单位 mm

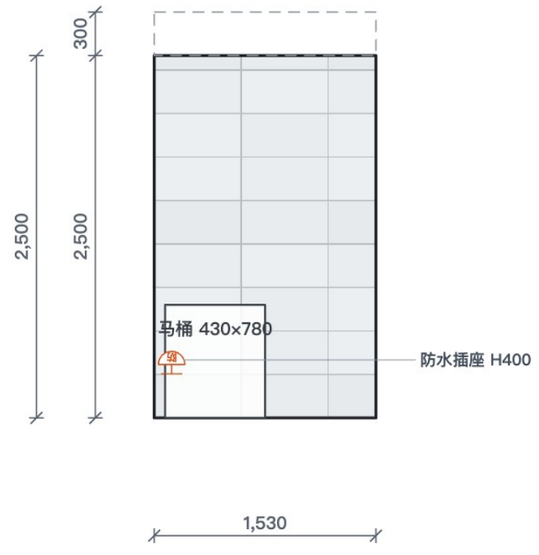

项目名称	比例	单位
D户型128㎡ · 四室两厅两卫	见尺寸	mm
图名	日期	图号
立面图 · 公卫干区 · 南立面 / 公卫湿区 · 东立面	2026/11/10	21 / 32


公卫干区 · 西立面

墙面：墙砖 · 踢脚线：无 · 吊顶后净高 2,500 · 净长 680 · 单位 mm

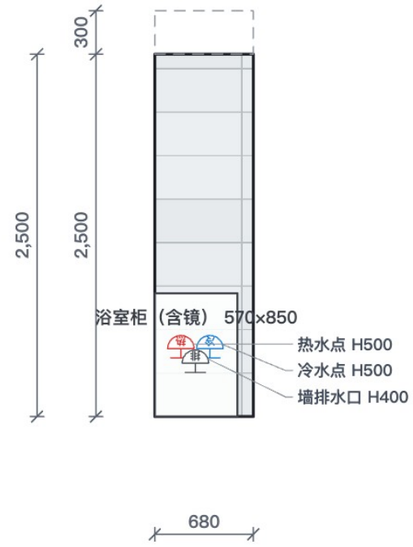

公卫干区 · 东立面


墙面：墙砖 · 踢脚线：无 · 吊顶后净高 2,500 · 净长 680 · 单位 mm

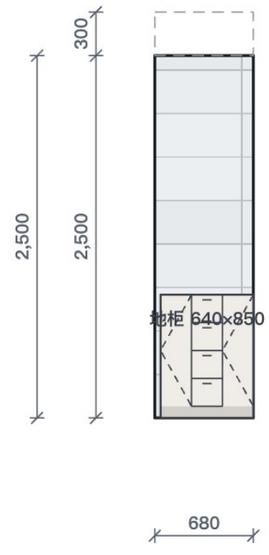

项目名称	比例	单位
D户型128㎡ · 四室两厅两卫	见尺寸	mm
图名	日期	图号
立面图 · 公卫干区 · 西立面 / 公卫干区 · 东立面	2026/11/10	22 / 32


公卫干区 · 北立面

墙面：墙砖 · 踢脚线：无 · 吊顶后净高 2,500 · 净长 1,570 · 单位 mm

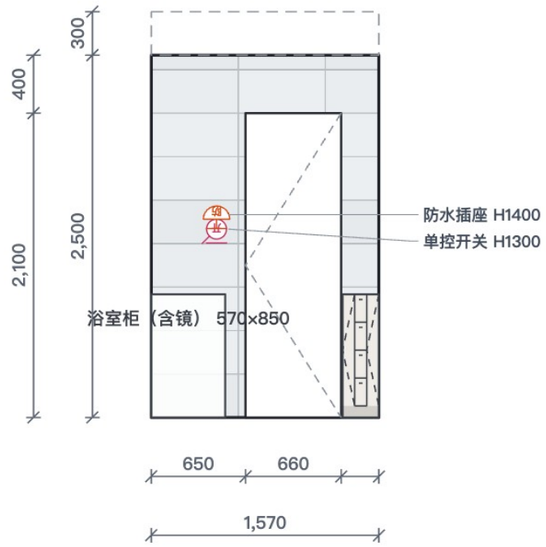

公卫湿区 · 南立面


墙面：墙砖 · 踢脚线：无 · 吊顶后净高 2,500 · 净长 1,570 · 单位 mm

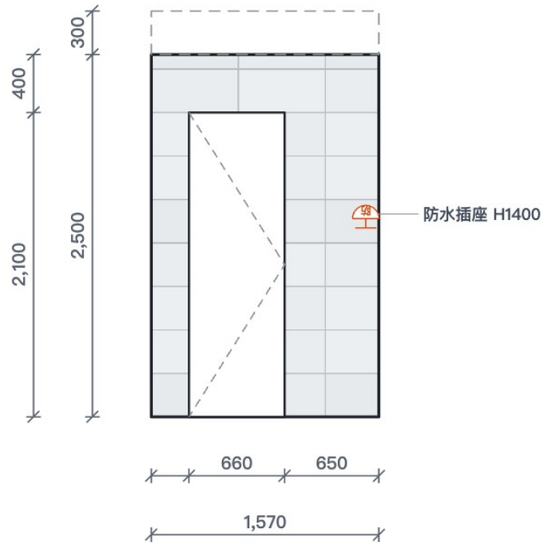

项目名称	比例	单位
D户型128㎡ · 四室两厅两卫	见尺寸	mm
图名	日期	图号
立面图 · 公卫干区 · 北立面 / 公卫湿区 · 南立面	2026/11/10	23 / 32


北次卧 · 南立面

墙面：奶咖乳胶漆 · 踢脚线：实木 80 · 吊顶后净高 2,800 · 净长 2,750 · 单位 mm

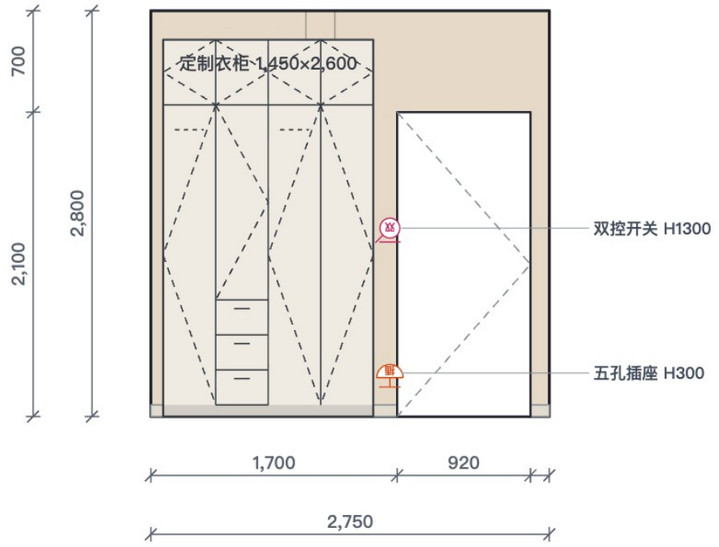

主卫 · 北立面


墙面：墙砖 · 踢脚线：无 · 吊顶后净高 2,500 · 净长 1,850 · 单位 mm

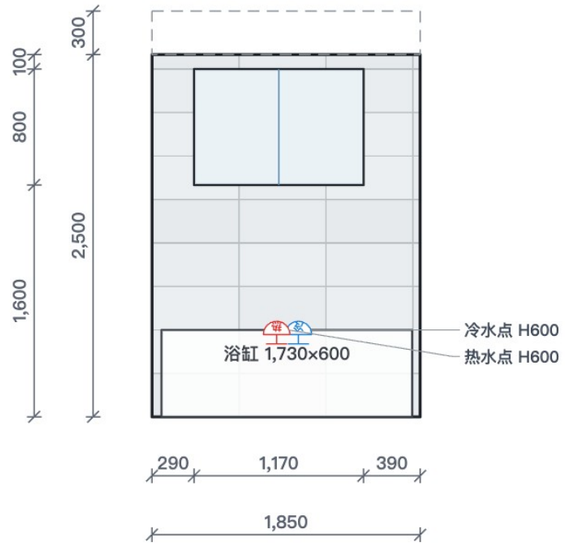

项目名称 D户型128㎡ · 四室两厅两卫		比例 见尺寸	单位 mm
图名 立面图 · 北次卧 · 南立面 / 主卫 · 北立面		日期 2026/11/10	图号 24 / 32


北次卧 · 东立面

墙面：奶咖乳胶漆 · 踢脚线：实木 80 · 吊顶后净高 2,800 · 净长 3,100 · 单位 mm

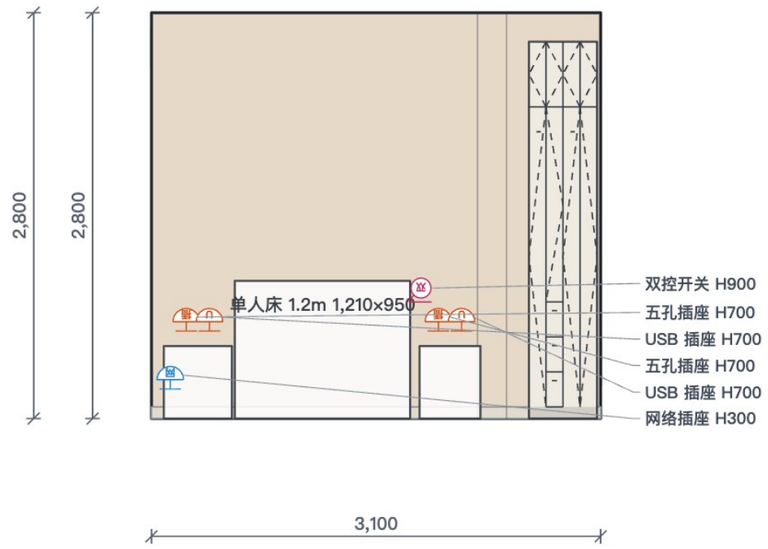

主卫 · 西立面


墙面：墙砖 · 踢脚线：无 · 吊顶后净高 2,500 · 净长 2,250 · 单位 mm

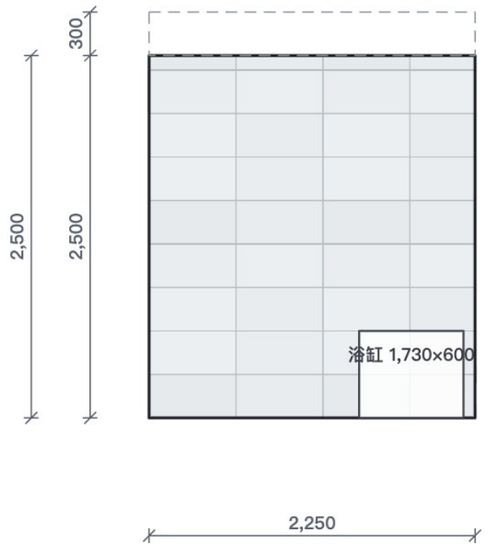

项目名称	比例	单位
D户型128㎡ · 四室两厅两卫	见尺寸	mm
图名	日期	图号
立面图 · 北次卧 · 东立面 / 主卫 · 西立面	2026/11/10	25 / 32


主卧 · 西立面

墙面：奶咖乳胶漆 · 踢脚线：实木 80 · 吊顶后净高 2,800 · 净长 650 · 单位 mm

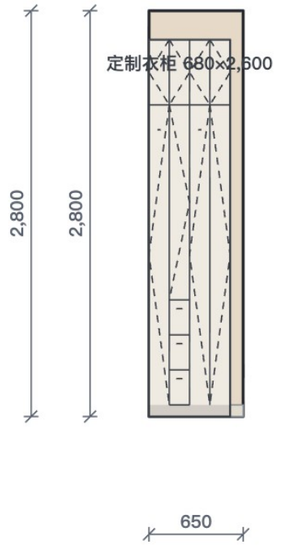

主卧 · 东立面


墙面：奶咖乳胶漆 · 踢脚线：实木 80 · 吊顶后净高 2,800 · 净长 5,050 · 单位 mm

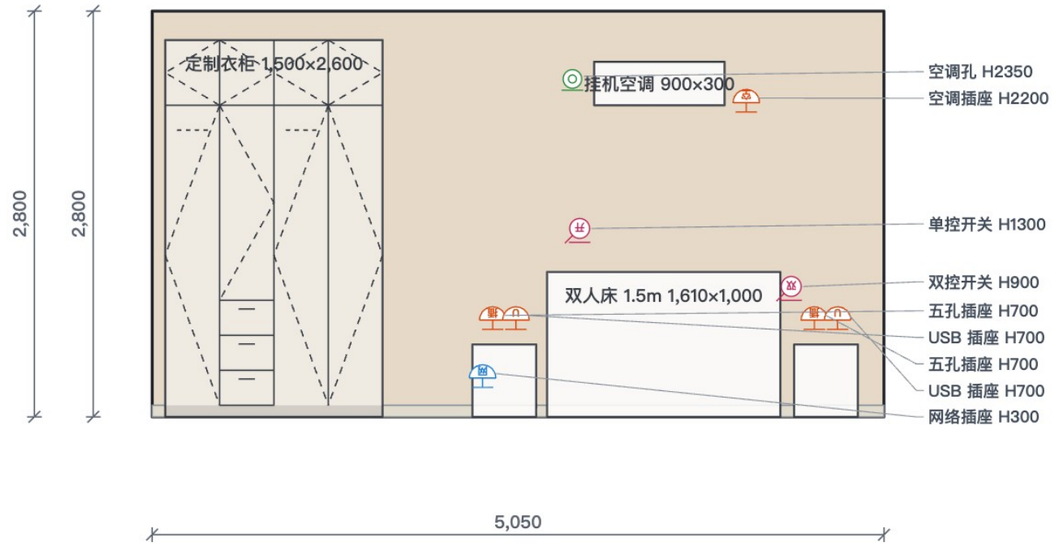

项目名称	比例	单位
D户型128㎡ · 四室两厅两卫	见尺寸	mm
图名	日期	图号
立面图 · 主卧 · 西立面 / 主卧 · 东立面	2026/11/10	26 / 32


主卧 · 北立面

墙面：奶咖乳胶漆 · 踢脚线：实木 80 · 吊顶后净高 2,800 · 净长 1,850 · 单位 mm

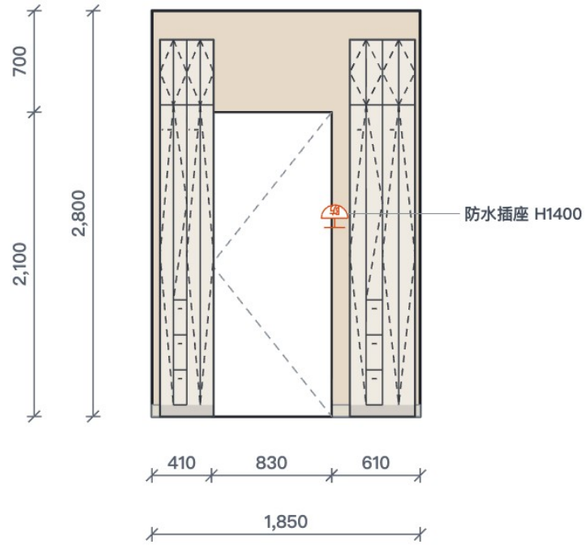

主卫 · 南立面


墙面：墙砖 · 踢脚线：无 · 吊顶后净高 2,500 · 净长 1,850 · 单位 mm

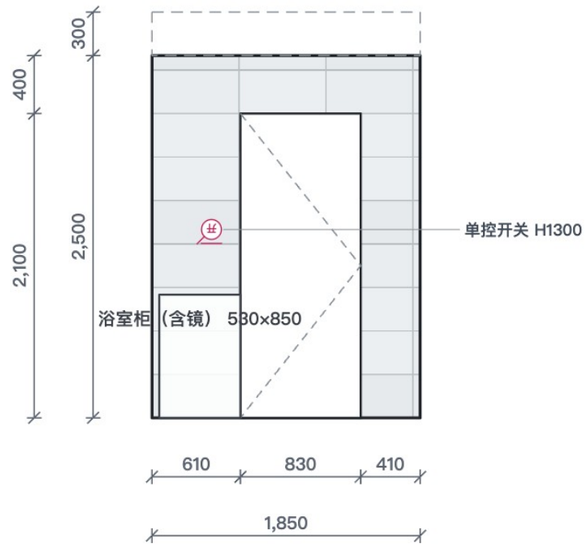

项目名称	比例	单位
D户型128㎡ · 四室两厅两卫	见尺寸	mm
图名	日期	图号
立面图 · 主卧 · 北立面 / 主卫 · 南立面	2026/11/10	27 / 32


主卧 · 北立面

墙面：奶咖乳胶漆 · 踢脚线：实木 80 · 吊顶后净高 2,800 · 净长 1,070 · 单位 mm

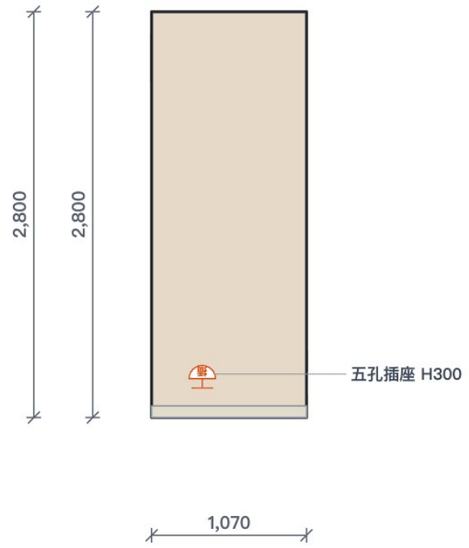

南次卧 · 南立面


墙面：奶咖乳胶漆 · 踢脚线：实木 80 · 吊顶后净高 2,800 · 净长 2,780 · 单位 mm

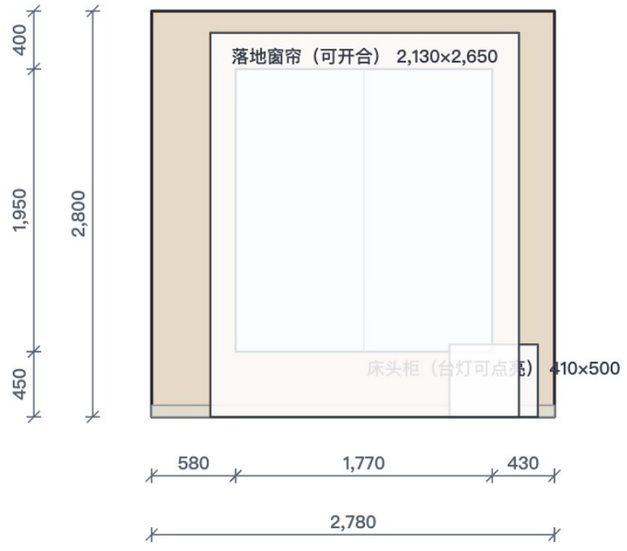

项目名称 D户型128㎡ · 四室两厅两卫		比例 见尺寸	单位 mm
图名 立面图 · 主卧 · 北立面 / 南次卧 · 南立面		日期 2026/11/10	图号 28 / 32


客餐厅 · 开放书房 · 东立面

墙面：奶咖乳胶漆 · 踢脚线：实木 80 · 吊顶后净高 2,800 · 净长 1,010 · 单位 mm

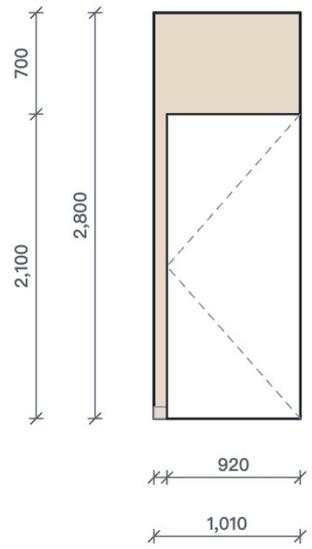

主卧 · 西立面


墙面：奶咖乳胶漆 · 踢脚线：实木 80 · 吊顶后净高 2,800 · 净长 4,200 · 单位 mm

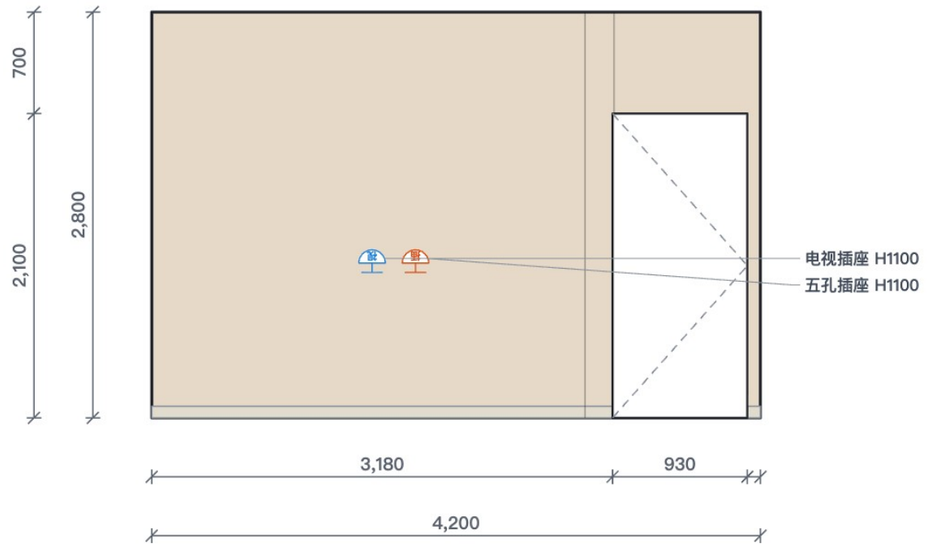

项目名称	比例	单位
D户型128㎡ · 四室两厅两卫	见尺寸	mm
图名	日期	图号
立面图 · 客餐厅 · 开放书房 · 东立面 / 主卧 · 西立面	2026/11/10	29 / 32


南次卧 · 东立面

墙面：奶咖乳胶漆 · 踢脚线：实木 80 · 吊顶后净高 2,800 · 净长 2,990 · 单位 mm

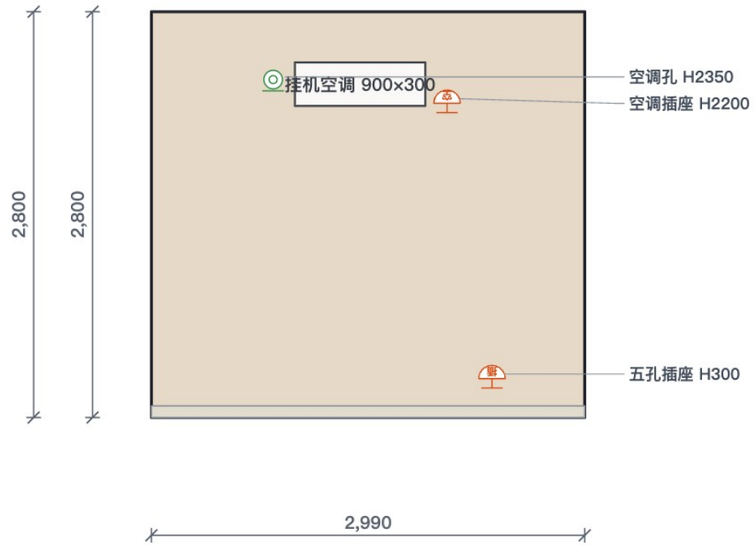

南次卧 · 北立面


墙面：奶咖乳胶漆 · 踢脚线：实木 80 · 吊顶后净高 2,800 · 净长 2,780 · 单位 mm

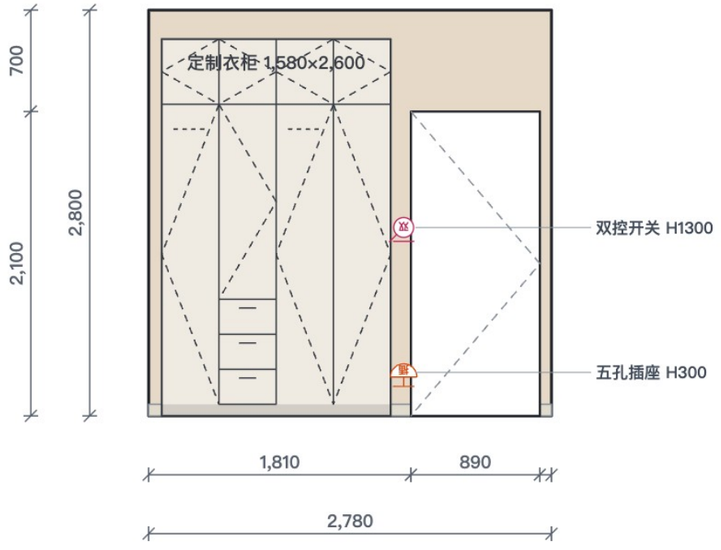

项目名称	比例	单位
D户型128㎡ · 四室两厅两卫	见尺寸	mm
图名	日期	图号
立面图 · 南次卧 · 东立面 / 南次卧 · 北立面	2026/11/10	30 / 32


客餐厅 · 开放书房 · 南立面

墙面：奶咖乳胶漆 · 踢脚线：实木 80 · 吊顶后净高 2,800 · 净长 2,780 · 单位 mm

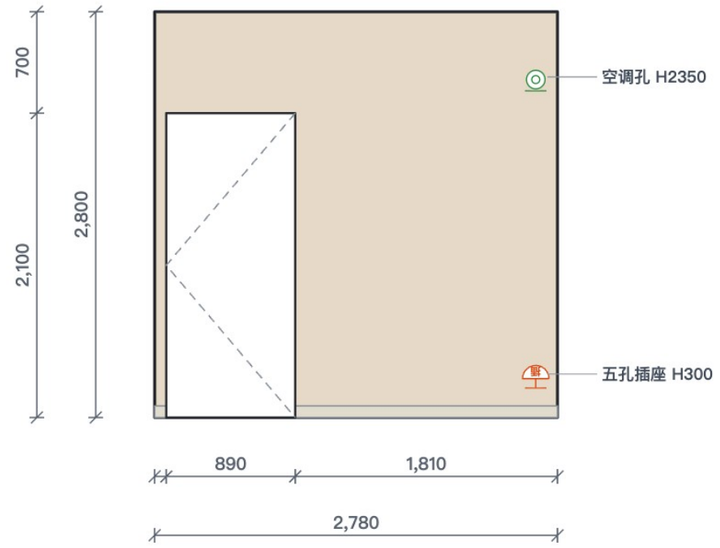

南次卧 · 西立面

墙面：奶咖乳胶漆 · 踢脚线：实木 80 · 吊顶后净高 2,800 · 净长 2,990 · 单位 mm

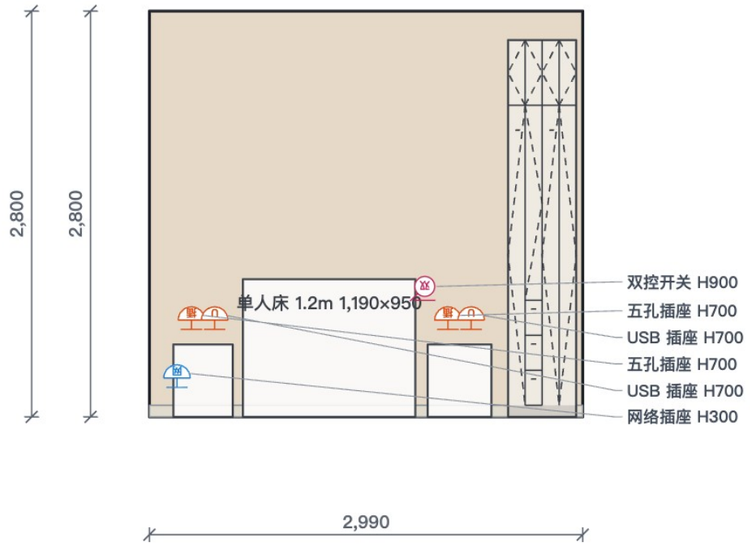

项目名称	比例	单位
D户型128㎡ · 四室两厅两卫	见尺寸	mm
图名	**日期**	**图号**
立面图 · 客餐厅 · 开放书房 · 南立面 / 南次卧 · 西立面	2026/11/10	31 / 32

工程量与报价单

合计 ¥128,746 · 单价为参考价 · 不含家具软装与电器

项目	数量	单位	单价(元)	合价(元)	明细
水电				**¥16,910**	
灯位	14	位	90	¥1,260	
弱电点位（网络/电视）	9	位	150	¥1,350	
强电点位（插座/开关，含线管）	61	位	120	¥7,320	
强电箱	1	个	1200	¥1,200	
弱电箱	1	个	800	¥800	
给水点位（含 PPR 管）	15	位	220	¥3,300	
排水点位（含 PVC 管）	3	位	160	¥480	
燃气改管（燃气公司施工）	2	位	300	¥600	
空调孔 / 新风口	5	位	120	¥600	
地面				**¥27,910**	
防滑地砖（含铺贴）	15.56	㎡	180	¥2,801	厨房 · 家政区 7.3、主卫 4.4、公卫湿区 2.6、公卫干区 1.2
橡木地板（含铺装）	17.68	㎡	260	¥4,597	北次卧 9.0、南次卧 8.7
地砖（自定义铺贴，按排砖片数，含铺贴）	61.44	㎡	220	¥13,517	客餐厅 · 开放书房 800×800 96片（整47/切46） 61.4
胡桃木地板（含铺装）	15.41	㎡	360	¥5,548	主卧 15.4
户外木塑（含安装）	6.29	㎡	230	¥1,447	阳台 6.3
墙面				**¥26,413**	
墙砖（含铺贴）	62.62	㎡	170	¥10,645	厨房 · 家政区 22.5、公卫湿区 14.1、主卫 17.8、公卫干区 8.2
奶咖乳胶漆（含找平）	173.94	㎡	45	¥7,827	北次卧 26.4、主卧 37.0、客餐厅 · 开放书房 66.0、阳台 17.6、南次卧 27.0
实木踢脚线	56.27	m	48	¥2,701	北次卧 10.0、主卧 14.0、客餐厅 · 开放书房 21.7、南次卧 10.6
卫生间防水（地面 + 墙面 1.8m）	69.87	㎡	75	¥5,240	厨房 · 家政区 28.1、主卫 18.9、公卫湿区 13.6、公卫干区 9.2
顶面				**¥4,819**	
石膏板平顶	14.68	㎡	135	¥1,982	厨房 · 家政区 6.9、主卫 4.2、公卫湿区 2.5、公卫干区 1.1
顶面乳胶漆	81.05	㎡	35	¥2,837	北次卧 8.5、客餐厅 · 开放书房 43.5、主卧 14.7、南次卧 8.3、阳台 6.0
门				**¥23,850**	
推拉门（含轨道）	3	樘	3200	¥9,600	
门洞包套	1	樘	850	¥850	
隐形推拉门（含预埋盒）	1	樘	4200	¥4,200	
室内单开门（含套）	4	樘	2300	¥9,200	
定制柜				**¥22,713**	
定制高柜（按投影面积）	13.55	㎡	950	¥12,873	定制衣柜 13.5
定制地柜（按延米）	0.64	m	1600	¥1,024	地柜 0.6
橱柜地柜（按延米）	3.04	m	1800	¥5,472	一字橱柜（可定制） 3.0
橱柜台面（石英石 / 岩板，按延米）	3.04	m	1100	¥3,344	一字橱柜（可定制） 3.0
工程直接费				**¥122,615**	
管理费 5%				**¥6,131**	
合计				**¥128,746**	

项目名称	比例	单位
D户型128㎡ · 四室两厅两卫	—	mm
图名	**日期**	**图号**
工程量与报价单	2026/11/10	32 / 32